
# P-016  P-16 Option A3, his frame (4 Nov)

Designtech Architects · Ar. Mamunur Rashid


Every phase of the design so far · 12 Nov 2026

**PHASE 0 · SITE · P-016 P-16 Rajbari Plot, the Real P-14**
**plot 1298 sft · inside setbacks 958 sft · road side faces N**


### PLATE1 · 1 step · plain rectangle

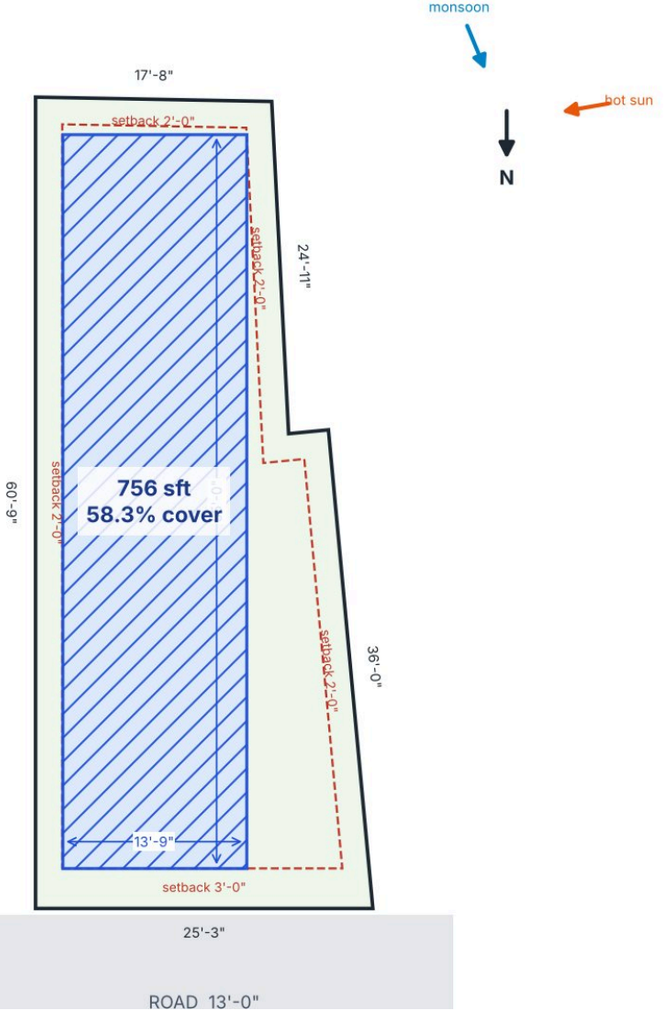


### PLATE2 · 2 steps · +131 sft

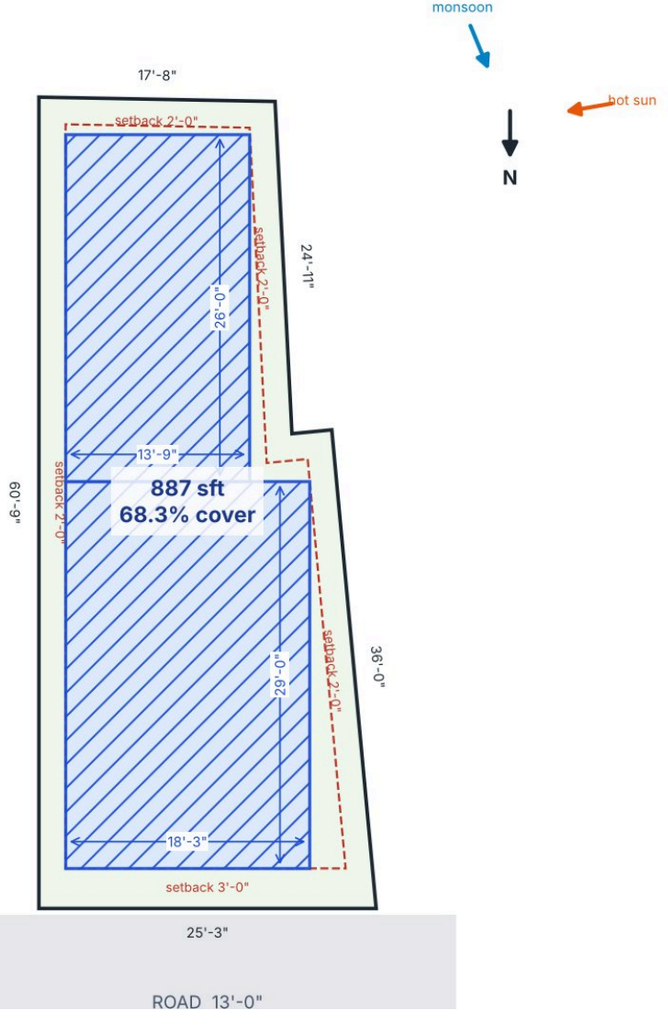



### STAGGER · 5 steps · +169 sft ★ CHOSEN

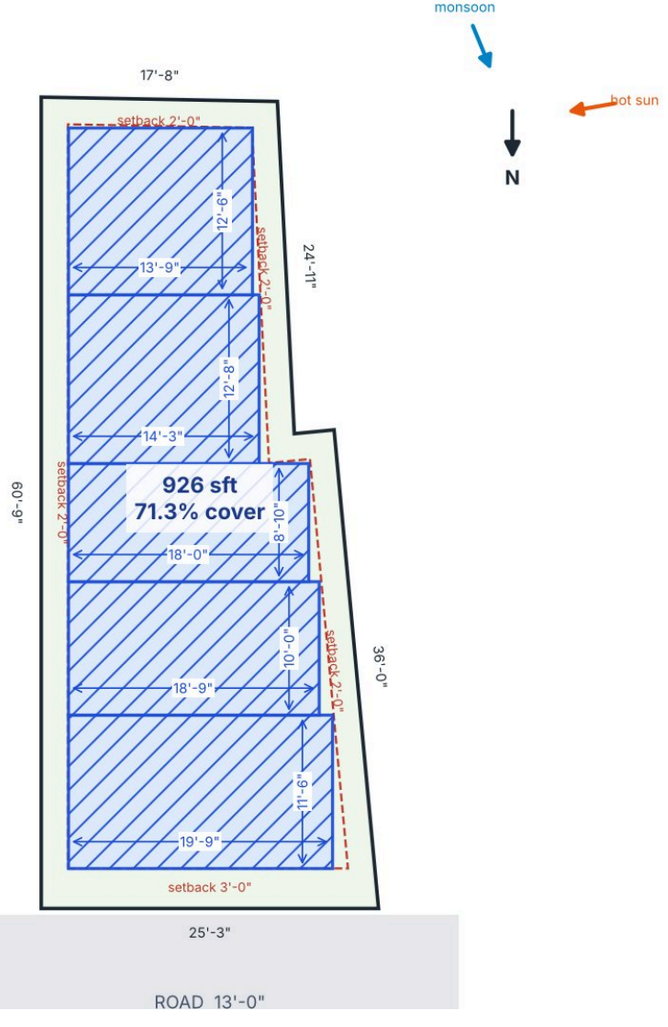

# Phase 1 · options · PHASE1 OPTIONS


**PHASE 1 · CORE, UNITS, WALL LINES · P-016 P-16 Option A2, his marks (4 Nov)**
**dashed grey = wall lines (where columns will land) · dotted blue = outside walls fit for toilet/kitchen shafts · red dot = deepest spot · yellow = stair half-landing window**

### OPTION 1 ★ RECOMMENDED · score 74.1 · gate PASS

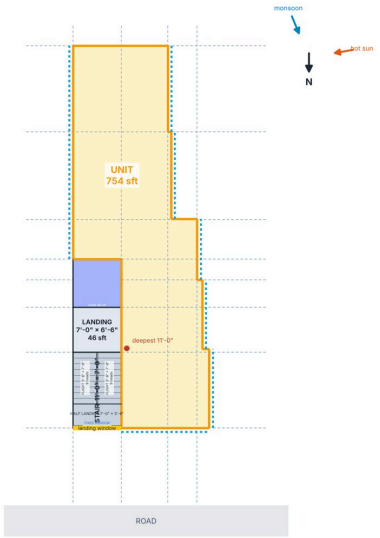



one unit of 754 sft
core 19% of the floor
stair's half landing on the N outside wall (window at the landing)
DNA: Unit takes no plan his way

### OPTION 2 · score 69.9 · gate PASS

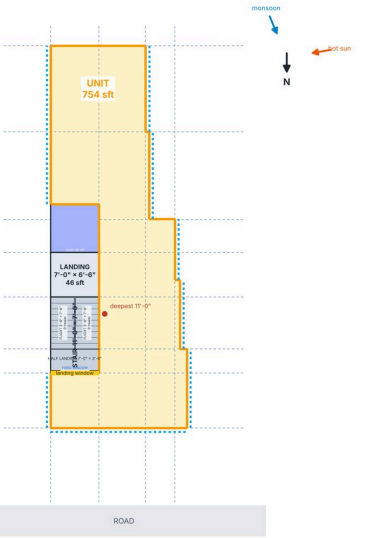



one unit of 754 sft
core 19% of the floor
stair lit from its side only — the half landing is inside
core side-mid — where his very-narrow plans put it (S-021, S-035, P-003) +6
DNA: Unit takes no plan his way

### OPTION 3 · score 69.9 · gate PASS

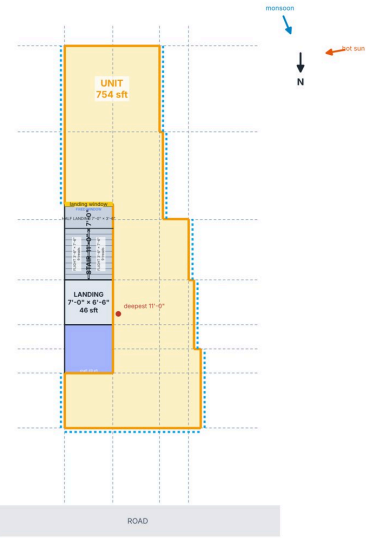



one unit of 754 sft
core 19% of the floor
stair lit from its side only — the half landing is inside
core side-mid — where his very-narrow plans put it (S-021, S-035, P-003) +6
DNA: Unit takes no plan his way

### OPTION 4 · score 60.6 · gate PASS

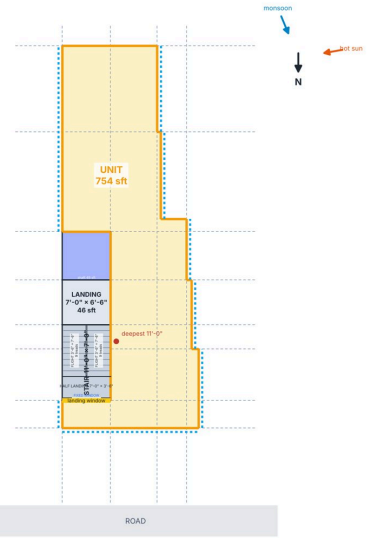



one unit of 754 sft
core 19% of the floor
stair lit from its side only — the half landing is inside
core side-mid — where his very-narrow plans put it (S-021, S-035, P-003) +6
Unit: 28 sft narrower than 7'-6" (hard to use)

### OPTION 6 · score 48.5 · gate PASS

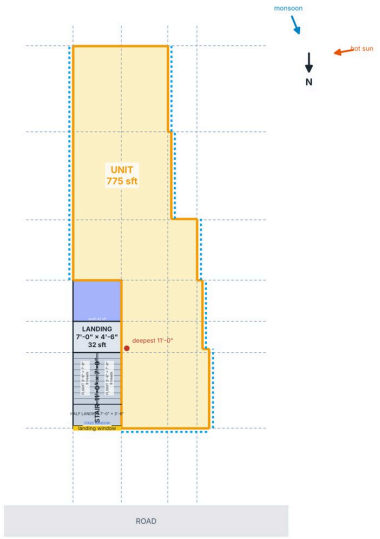



his P-014's bones mirrored (his order 4 Nov 13:49): the core in the front corner on the EAST (P-014: west) — the stair's half landing on the road face with its window, the landing, then the lift; the flat runs in rows behind it: the front bedroom on the WEST now (its face needs the elevation's sun treatment), the drawing-cum-dining beside the core, the wet row, the bedrooms behind; the plate staggered along the angled west boundary room row by room (his TG-04 STAGGER)
Unit: a long unit (2.8 × as long as wide) — rooms can't all open off the living (rule 76)
one unit of 775 sft
core 16% of the floor
stair's half landing on the N outside wall (window at the landing)

### OPTION 8 · score 48.5 · gate PASS

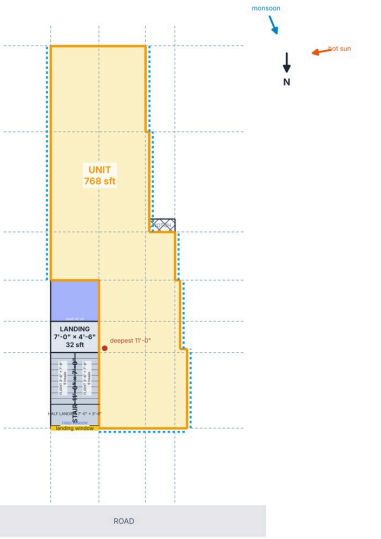



his P-014's bones mirrored (his order 4 Nov 13:49): the core in the front corner on the EAST (P-014: west) — the stair's half landing on the road face with its window, the landing, then the lift; the flat runs in rows behind it: the front bedroom on the WEST now (its face needs the elevation's sun treatment), the drawing-cum-dining beside the core, the wet row, the bedrooms behind; the plate staggered along the angled west boundary room row by room (his TG-04 STAGGER)
Unit: a long unit (2.8 × as long as wide) — rooms can't all open off the living (rule 76)
one unit of 768 sft
core 16% of the floor
stair's half landing on the N outside wall (window at the landing)

### OPTION 9 · score 51.7 · gate PASS · CHOSEN

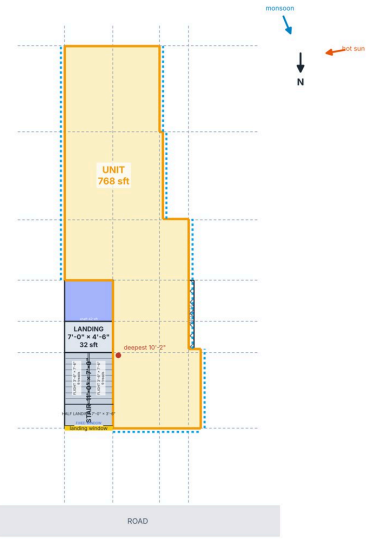


his P-014's bones mirrored (his order 4 Nov 13:49): the core in the front corner on the EAST (P-014: west) — the stair's half landing on the road face with its window, the landing, then the lift; the flat runs in rows behind it: the front bedroom on the WEST now (its face needs the elevation's sun treatment), the drawing-cum-dining beside the core, the wet row, the bedrooms behind; the plate staggered along the angled west boundary room row by room (his TG-04 STAGGER) set 213 (his marks 4 Nov 15:50 on Option A): the hatched step pocket joined to the living as the fridge bay (no thin walls), the Shelf's strip given to his west balcony
Unit: a long unit (2.8 × as long as wide) — rooms can't all open off the living (rule 76)
one unit of 768 sft
core 16% of the floor

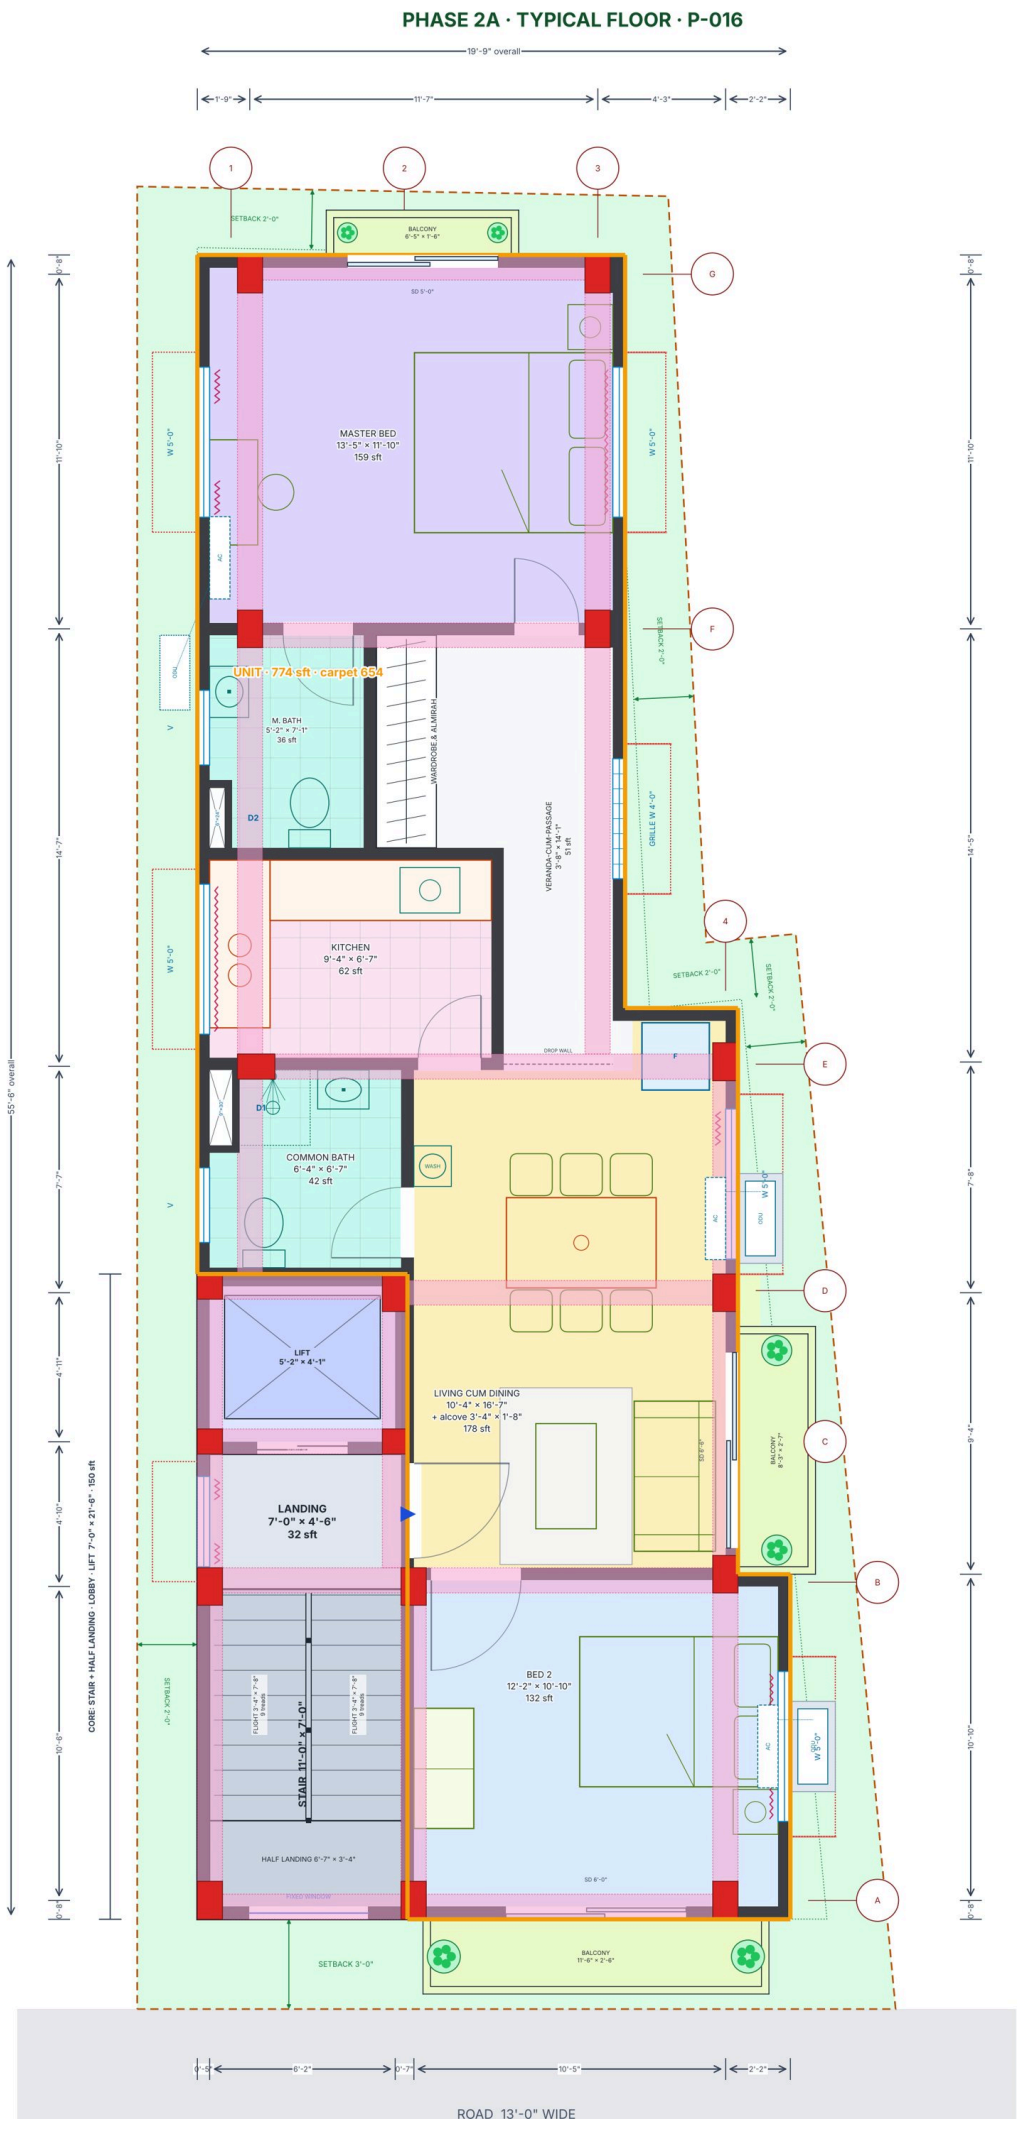


## ROOMS · Typical floor

inside sizes, face to face

**Bed 2**
10'-10" × 12'-2" · 132 sft

**Living cum Dining**
10'-4" × 16'-7" · 172 sft


**Common Bath**
6'-4" × 6'-7" · 42 sft

**Kitchen**
6'-7" × 9'-4" · 62 sft

**Veranda-cum-passage**
3'-8" × 14'-1" · 51 sft

**Master Bed Bath**
5'-2" × 7'-1" · 36 sft

**Master Bed**
11'-10" × 13'-5" · 159 sft

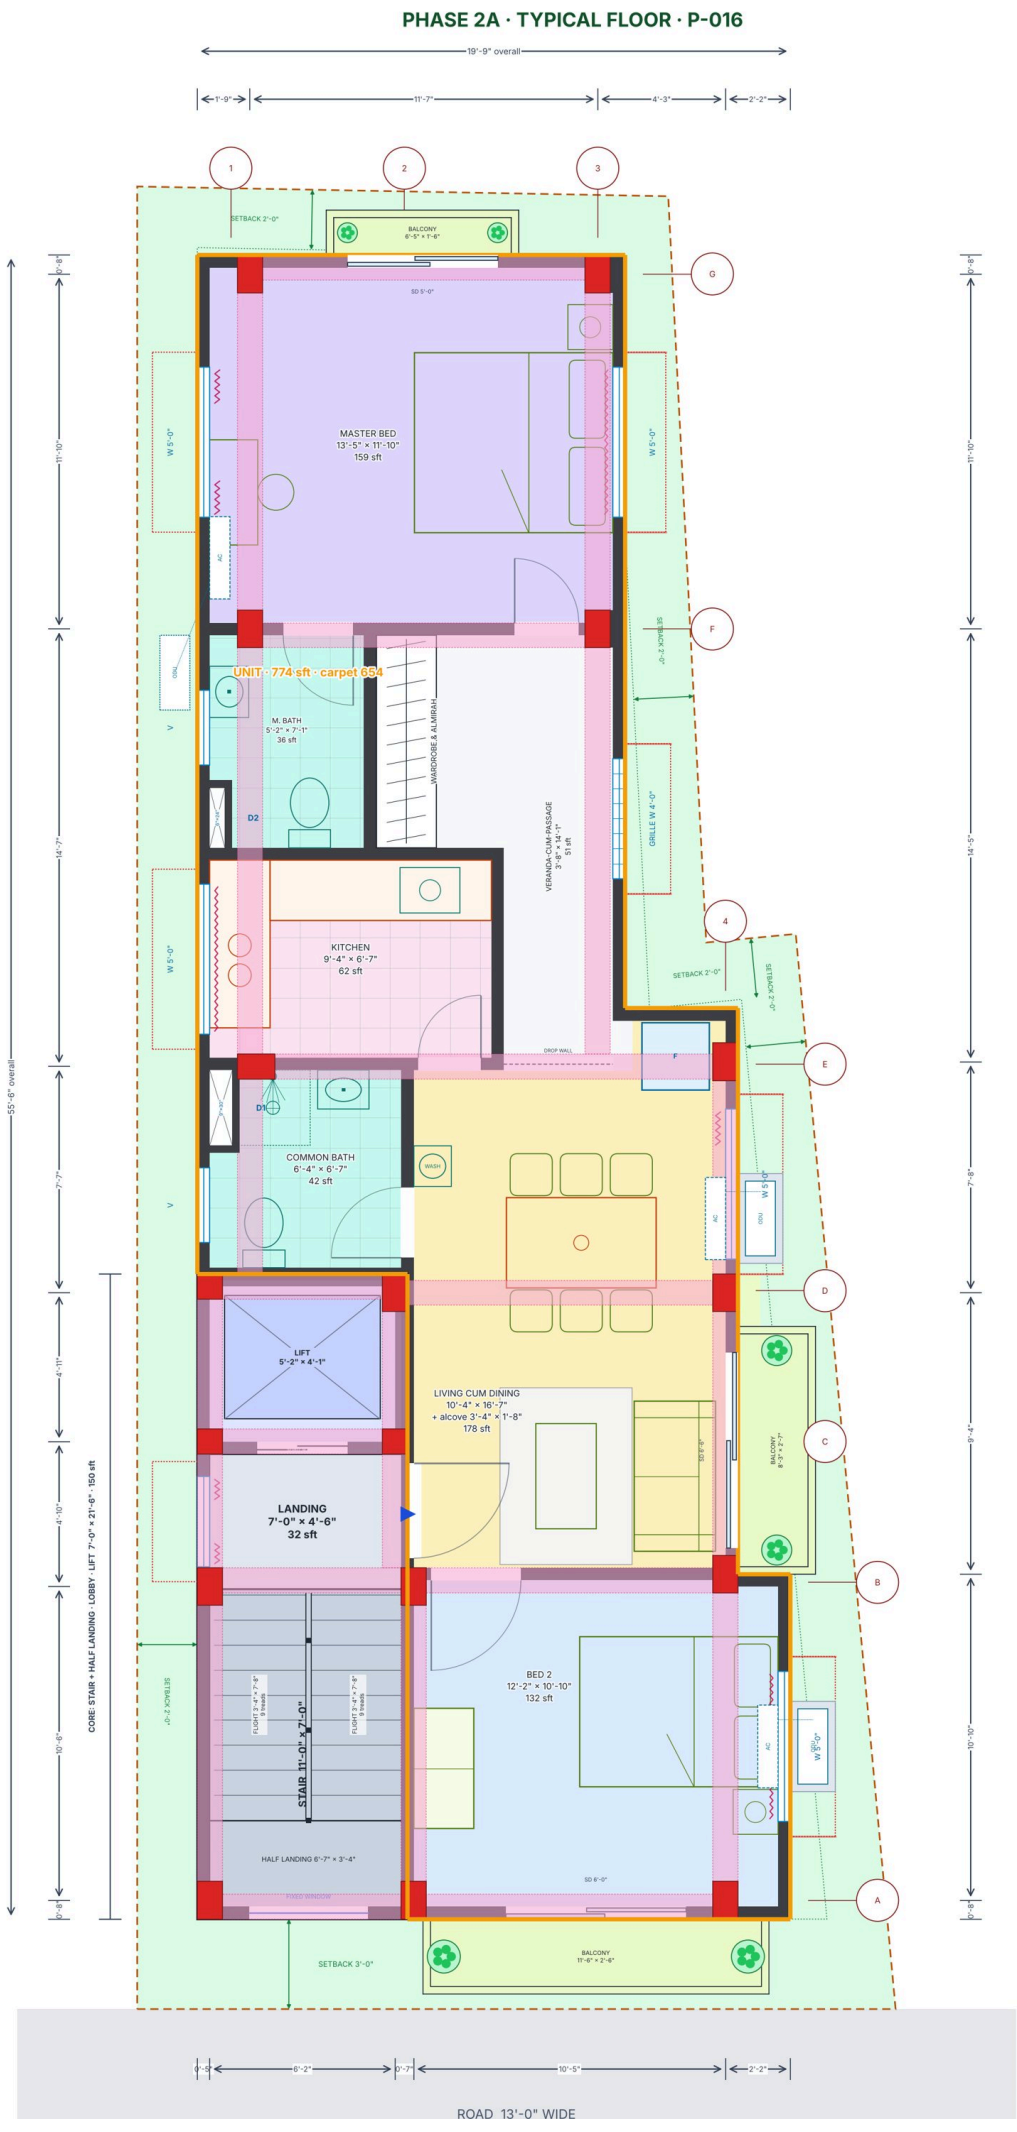


## ROOMS · Typical floor

inside sizes, face to face

**Bed 2**
10'-10" × 12'-2" · 132 sft

**Living cum Dining**
10'-4" × 16'-7" · 172 sft


**Common Bath**
6'-4" × 6'-7" · 42 sft

**Kitchen**
6'-7" × 9'-4" · 62 sft

**Veranda-cum-passage**
3'-8" × 14'-1" · 51 sft

**Master Bed Bath**
5'-2" × 7'-1" · 36 sft

**Master Bed**
11'-10" × 13'-5" · 159 sft

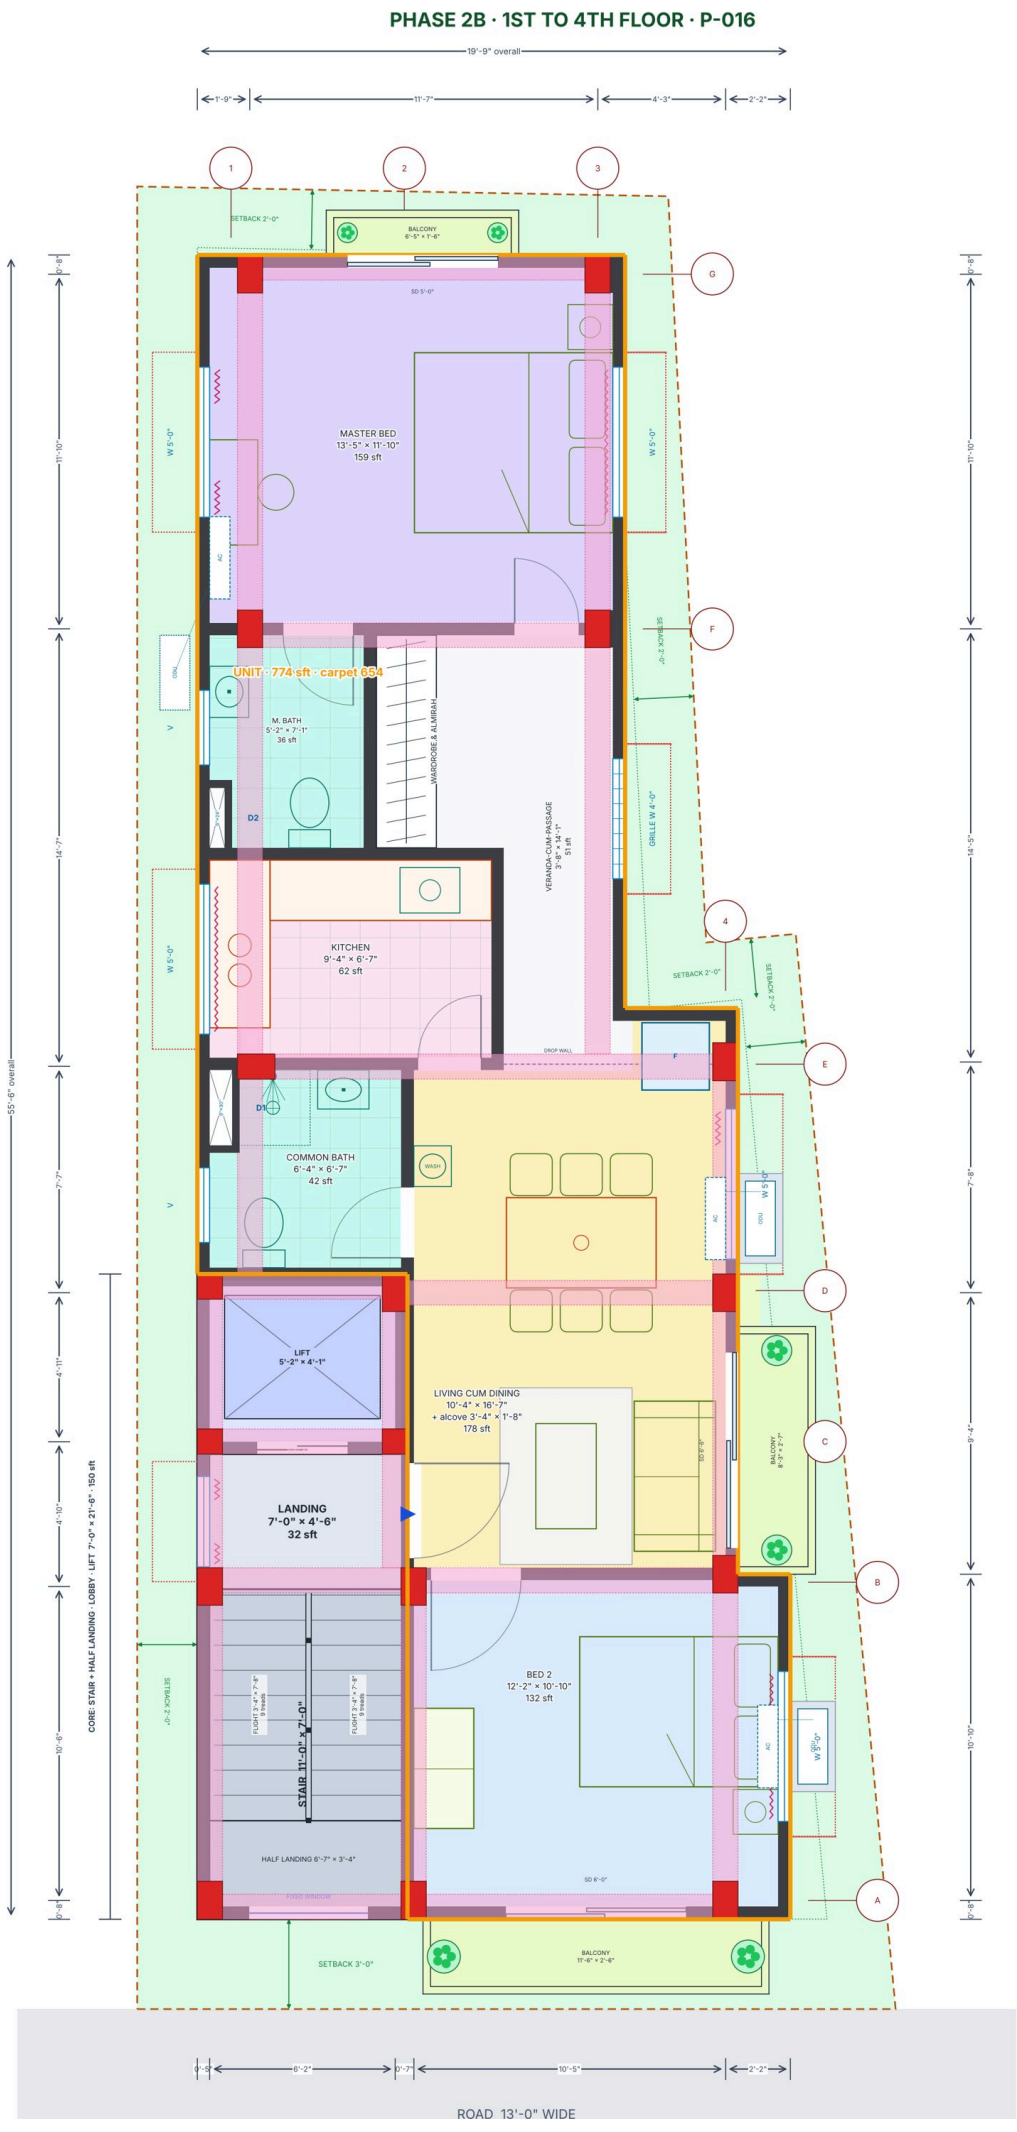


## ROOMS · Typical floor

inside sizes, face to face

**Bed 2**
10'-10" × 12'-2" · 132 sft

**Living cum Dining**
10'-4" × 16'-7" · 172 sft


**Common Bath**
6'-4" × 6'-7" · 42 sft

**Kitchen**
6'-7" × 9'-4" · 62 sft

**Veranda-cum-passage**
3'-8" × 14'-1" · 51 sft

**Master Bed Bath**
5'-2" × 7'-1" · 36 sft

**Master Bed**
11'-10" × 13'-5" · 159 sft

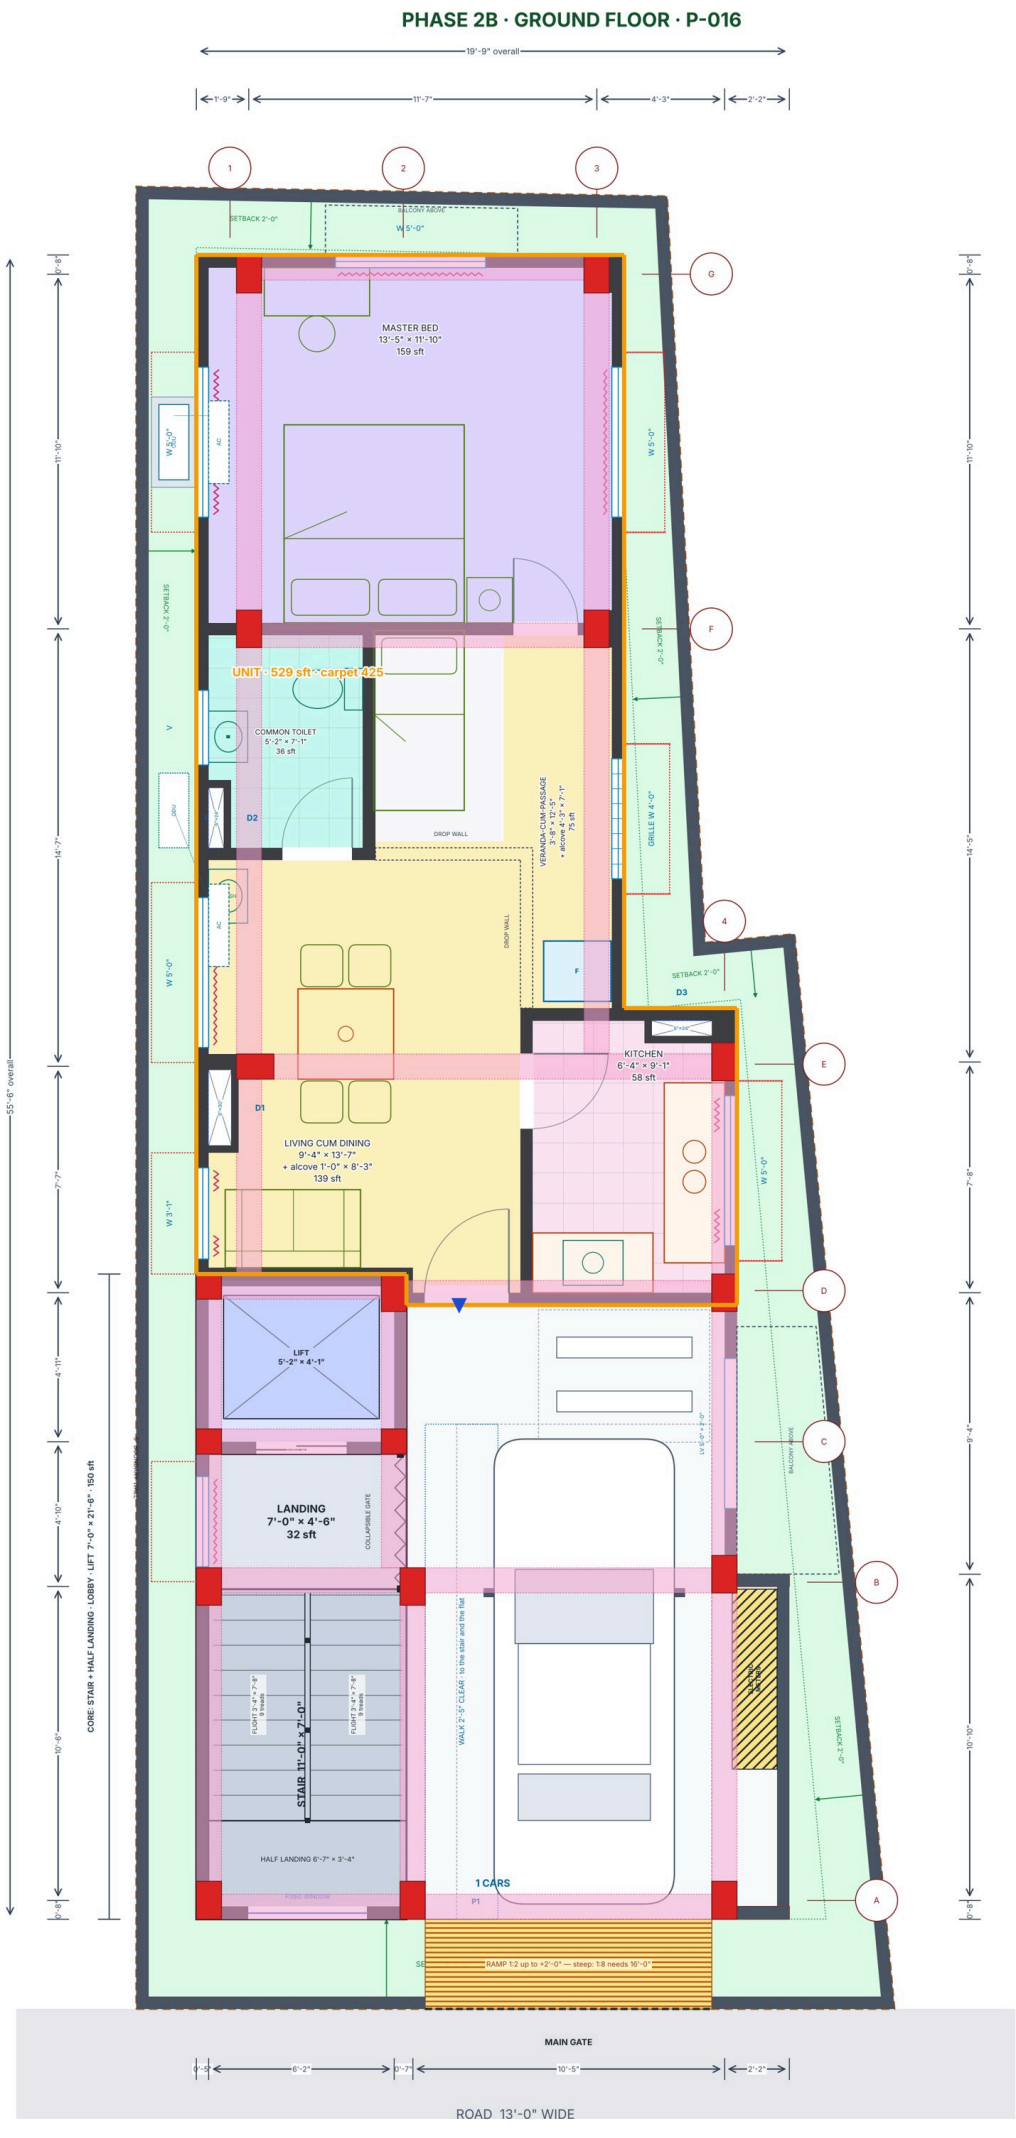


## ROOMS · Ground floor

inside sizes, face to face


**Living cum Dining**
9'-4" × 13'-7" · 127 sft

**Veranda-cum-passage**
3'-8" × 12'-5" · 45 sft

**Common Toilet**
5'-2" × 7'-1" · 36 sft

**Master Bed**
11'-10" × 13'-5" · 159 sft

**Kitchen**
6'-4" × 9'-1" · 58 sft

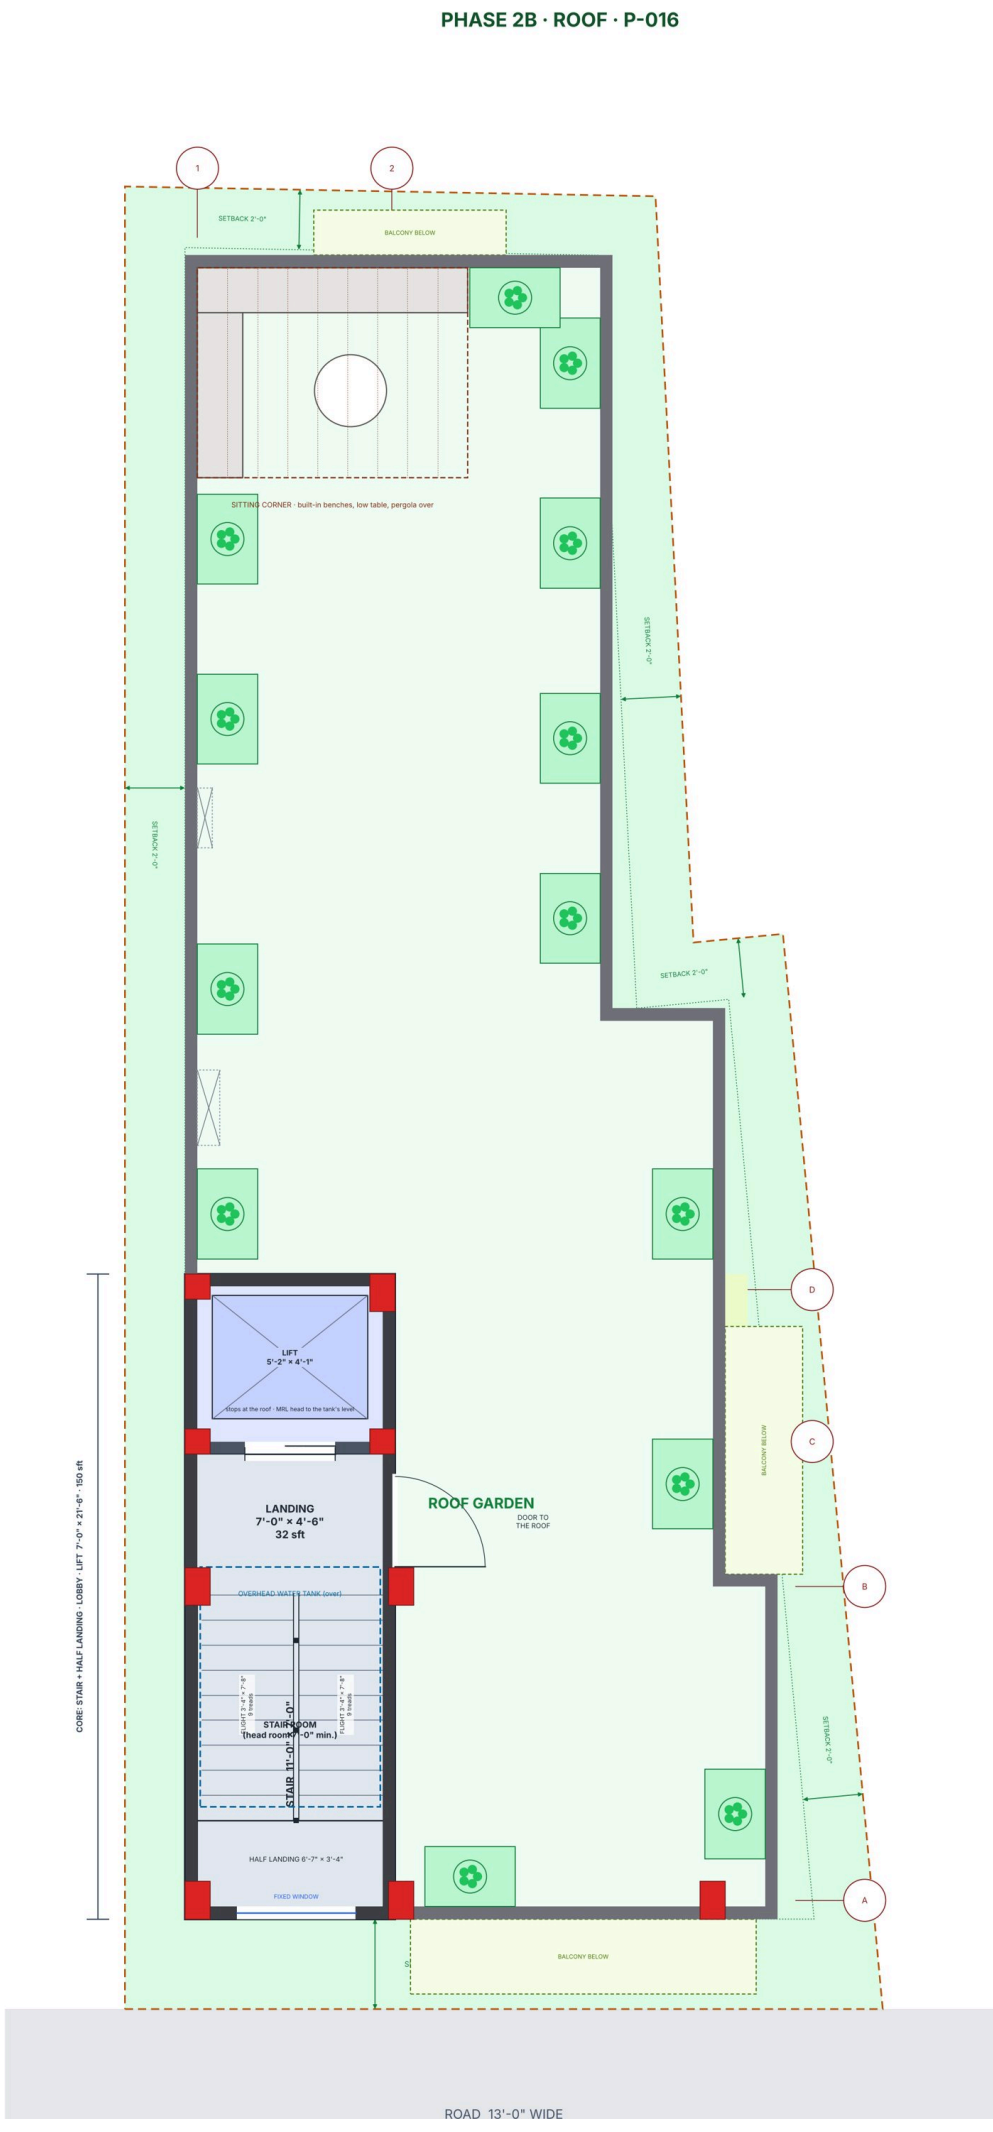


## ROOMS · Typical floor

inside sizes, face to face

**Bed 2**
10'-10" × 12'-2" · 132 sft

**Living cum Dining**
10'-4" × 16'-7" · 172 sft

**Common Bath**
6'-4" × 6'-7" · 42 sft


**Kitchen**
6'-7" × 9'-4" · 62 sft

**Veranda-cum-passage**
3'-8" × 14'-1" · 51 sft


**Master Bed Bath**
5'-2" × 7'-1" · 36 sft

**Master Bed**
11'-10" × 13'-5" · 159 sft


## PHASE 3 · AXONOMETRIC FROM THE ROAD, RIGHT · P-016

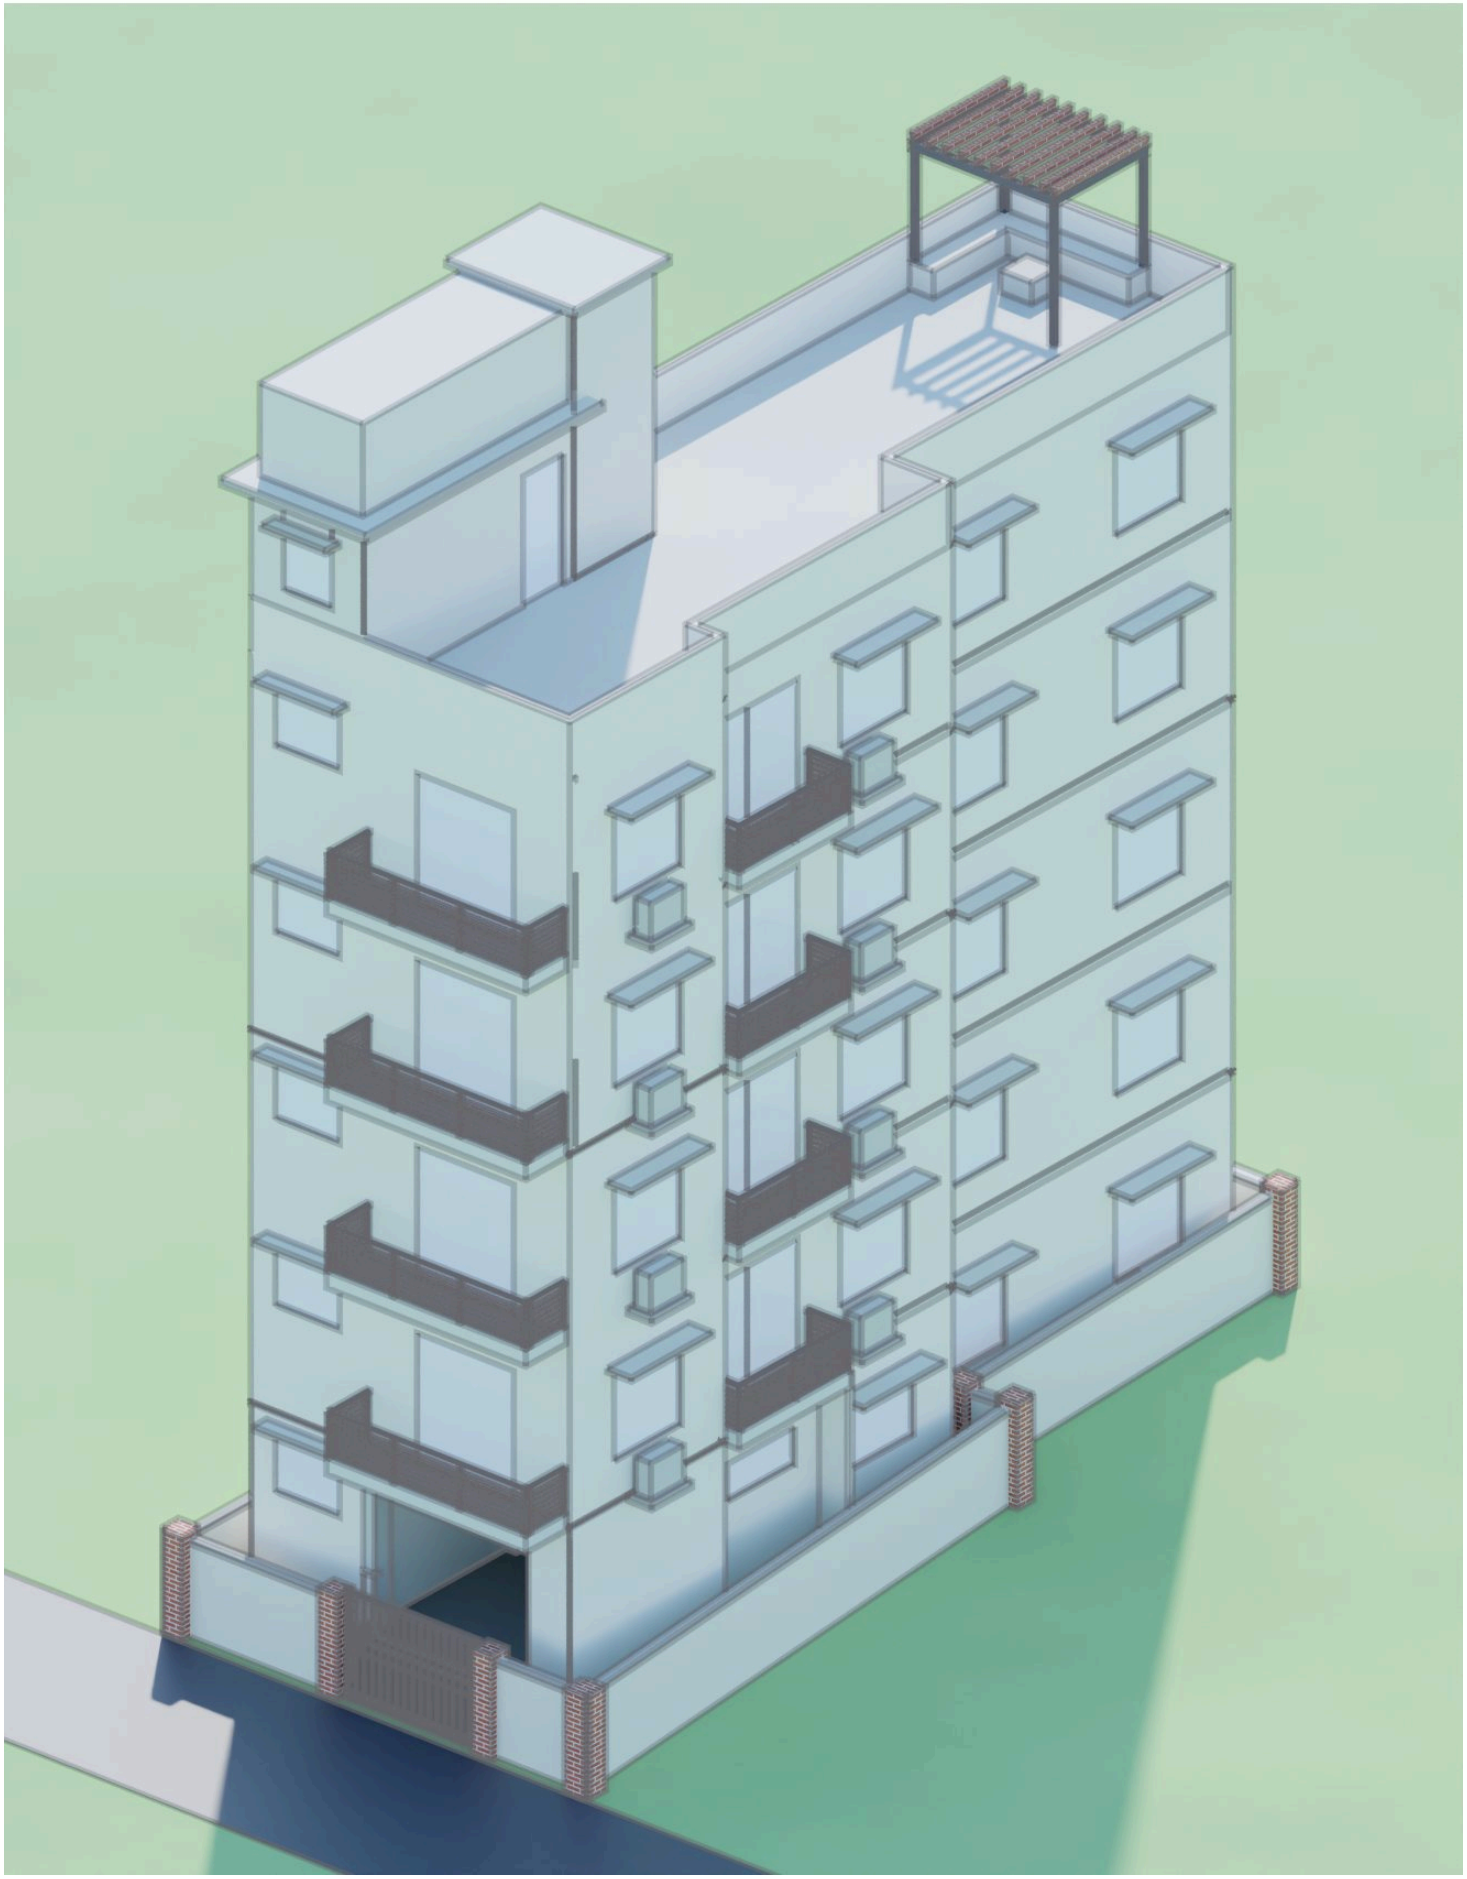


## PHASE 3 · AXONOMETRIC FROM THE ROAD, LEFT · P-016

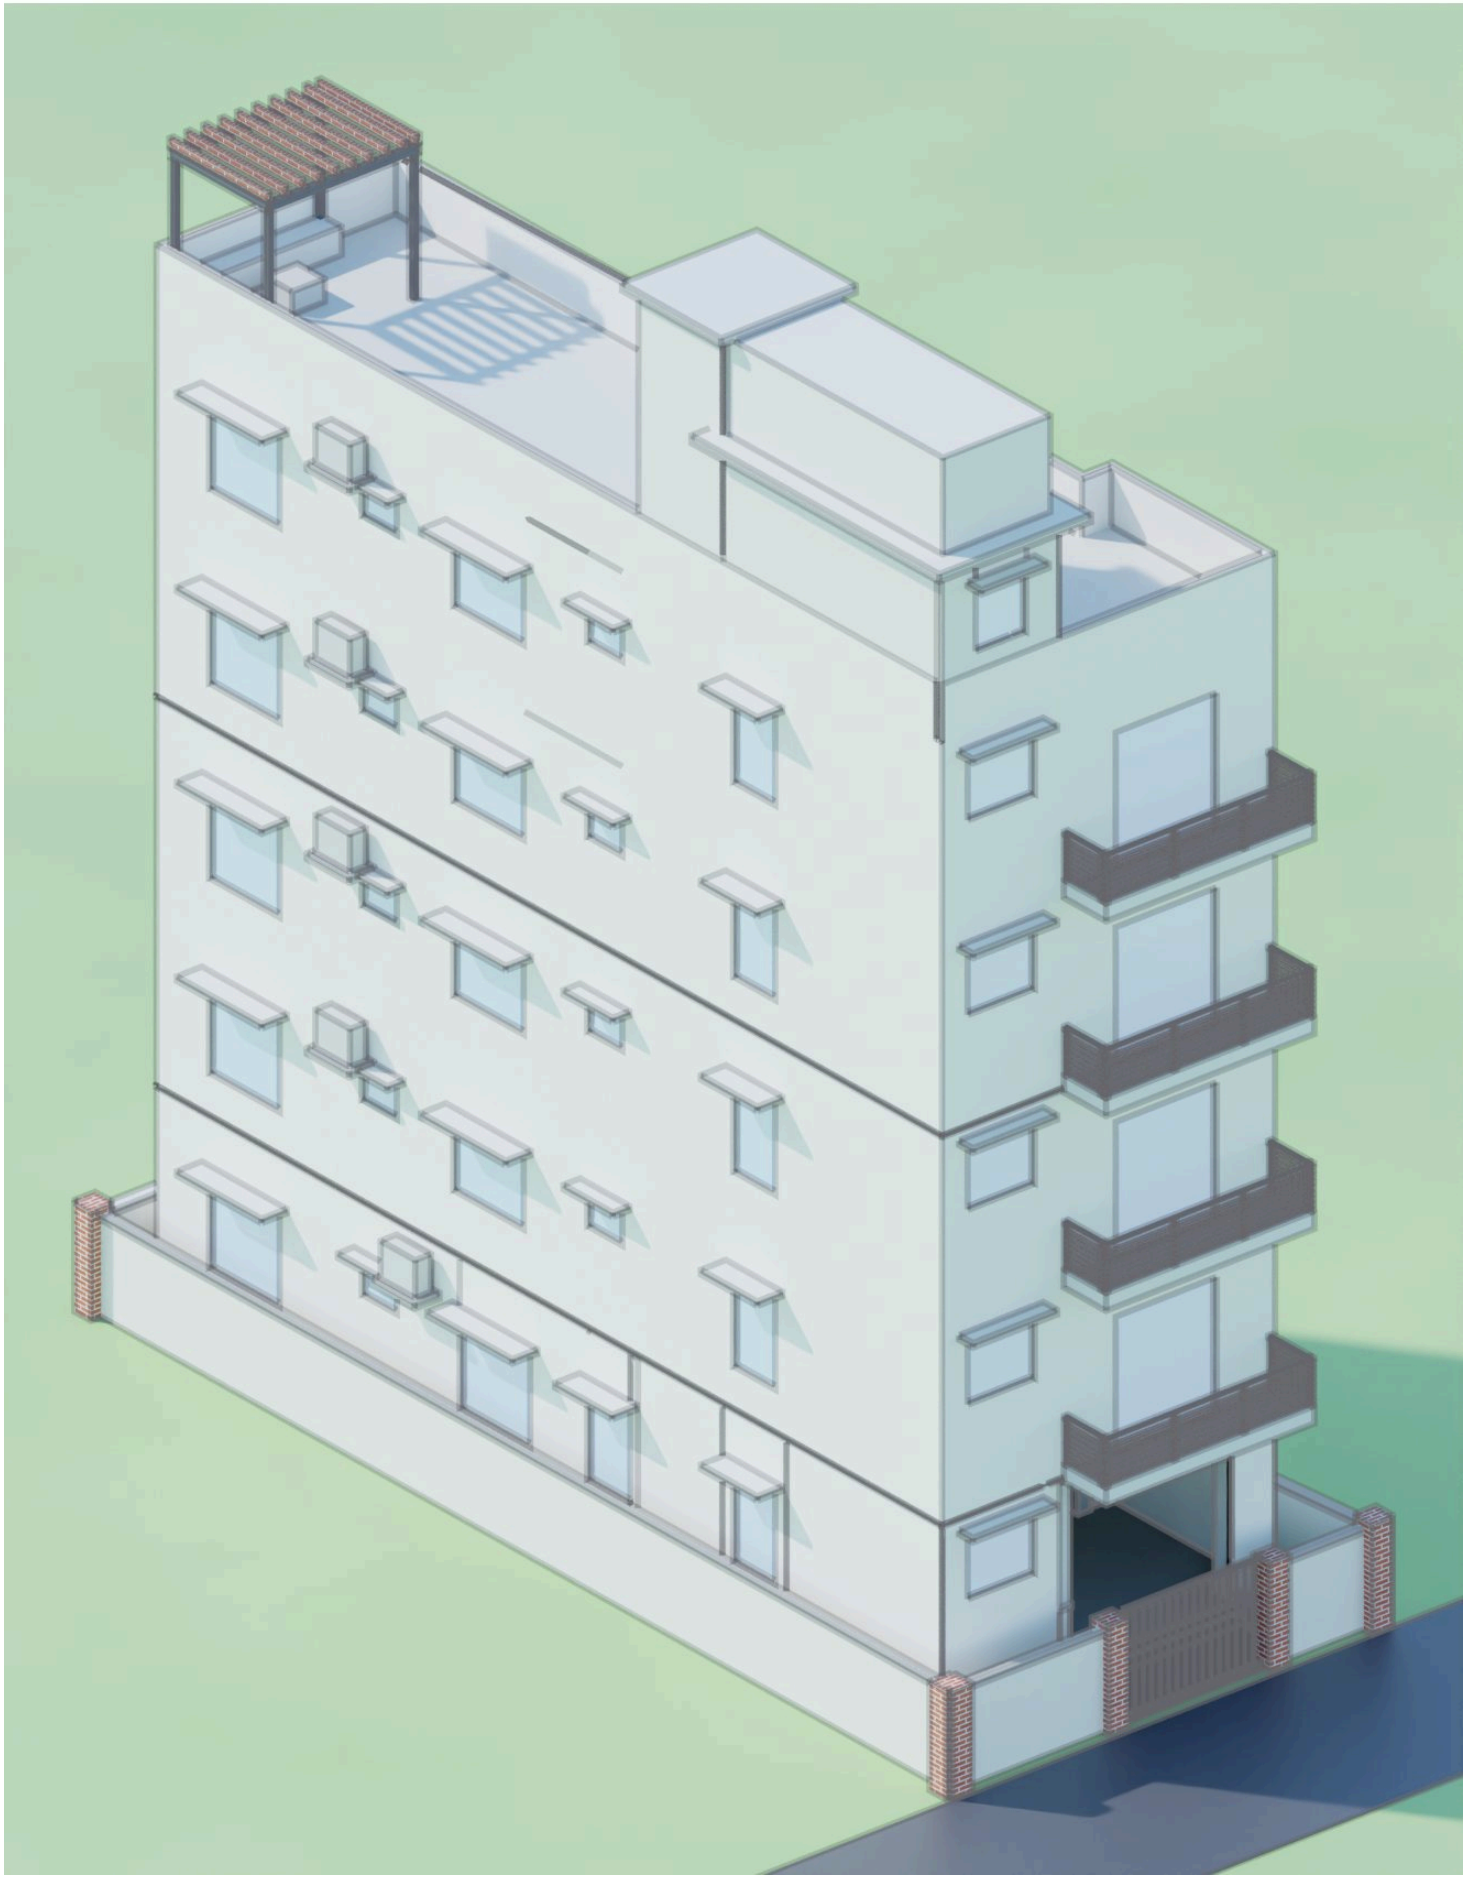


# PHASE 3 · RIGHT SIDE ELEVATION · P-016

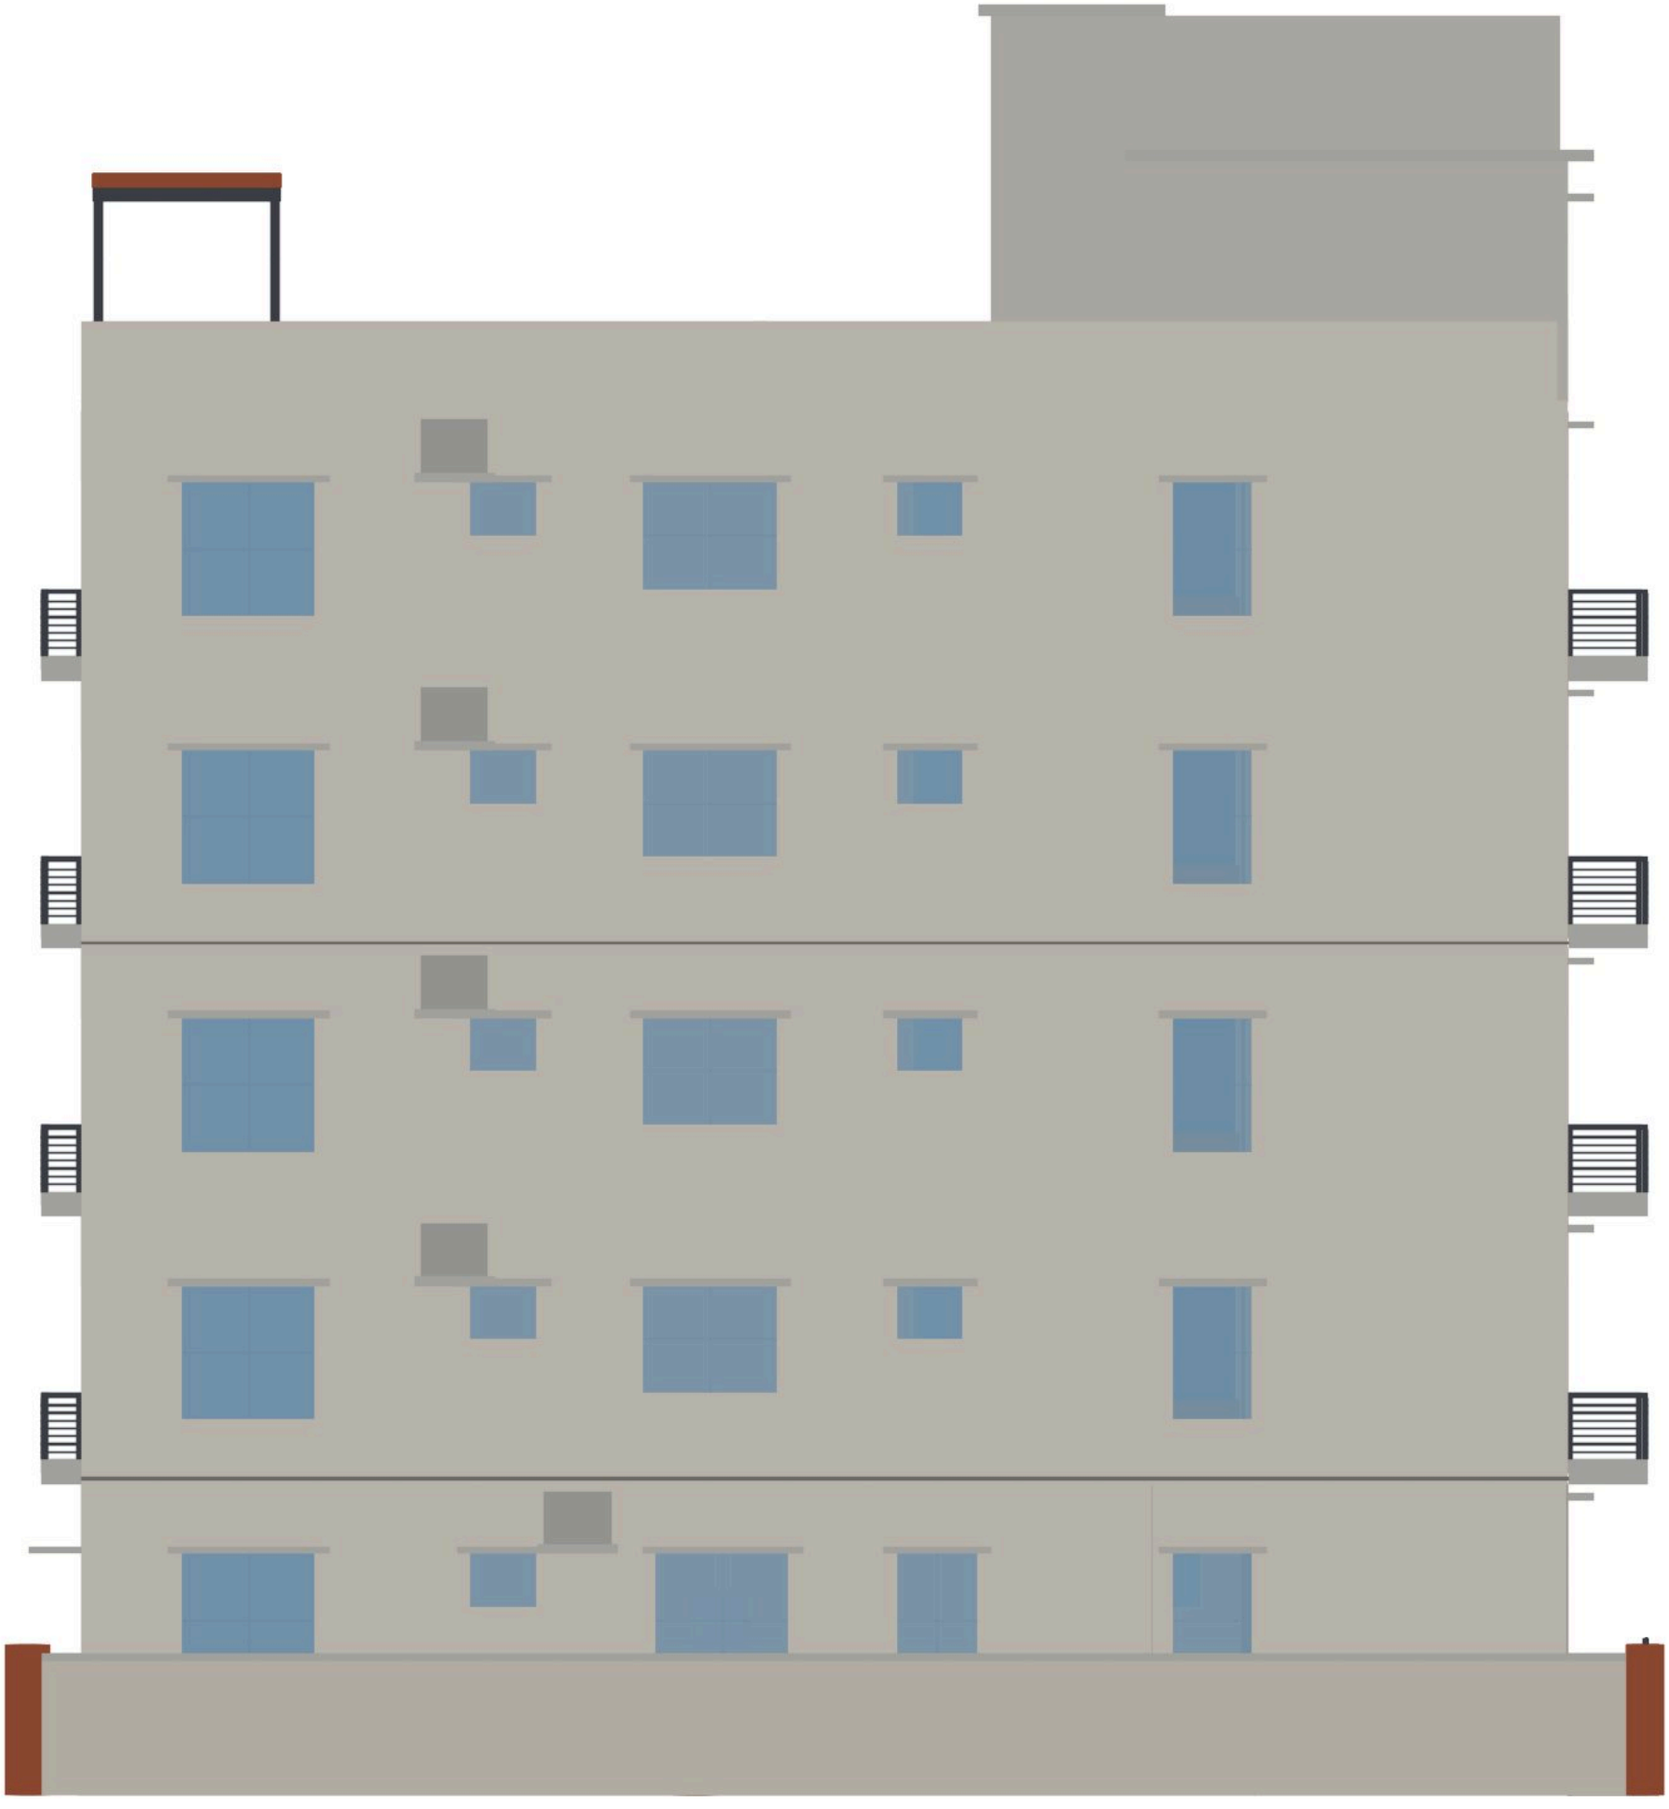


PHASE 3 · REAR ELEVATION · P-016

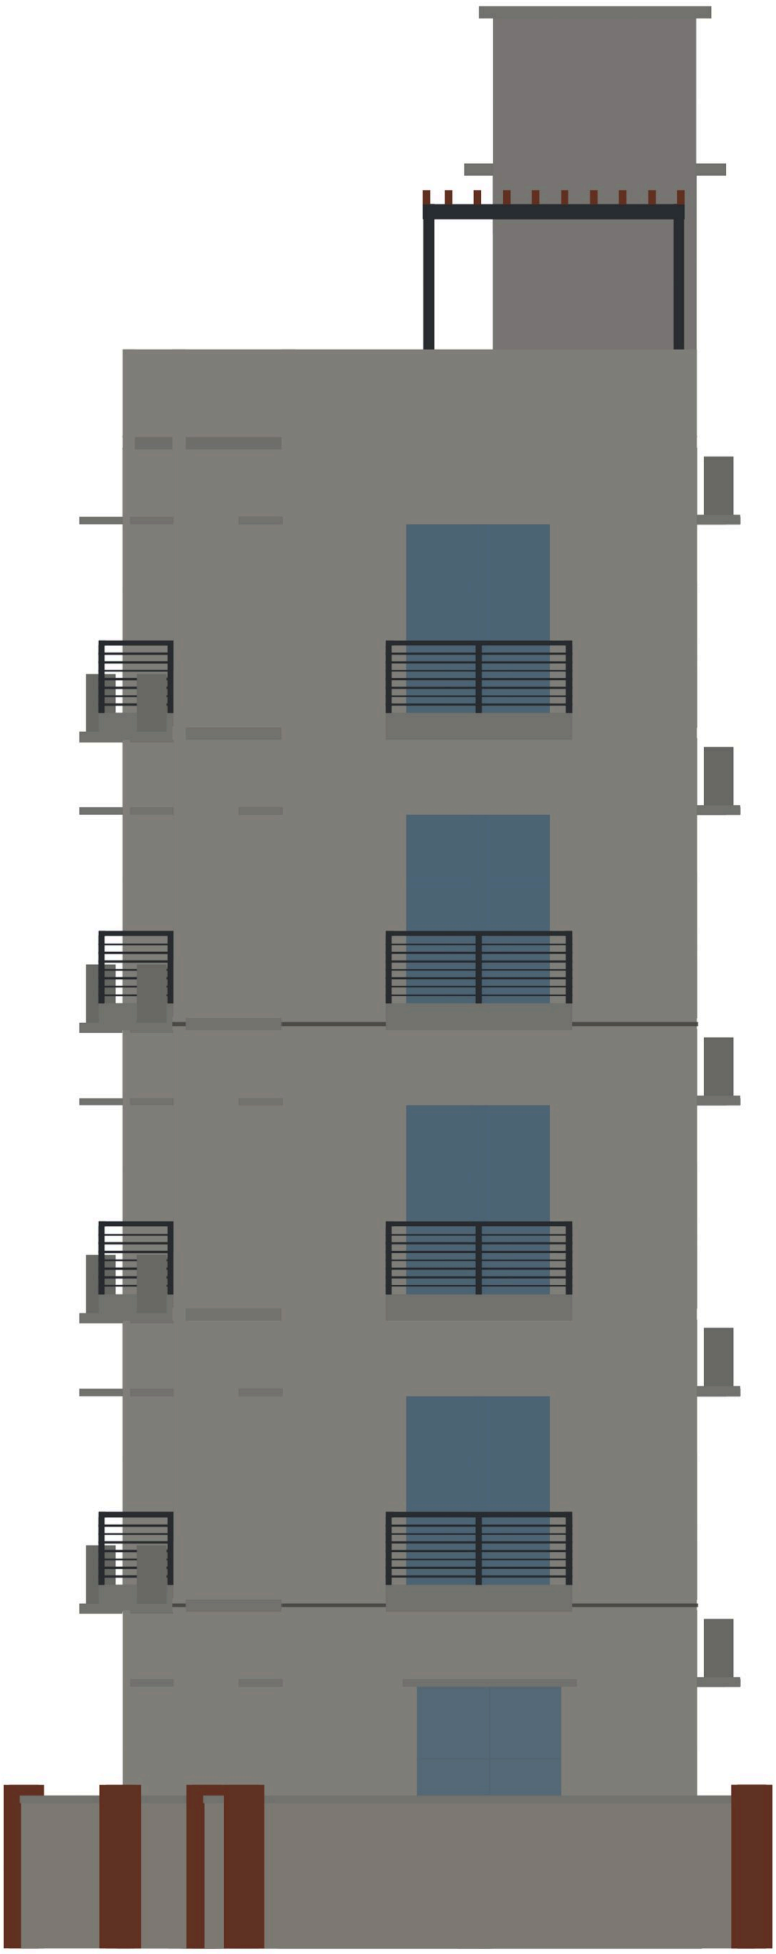

PHASE 3 · FRONT ELEVATION (ROAD) · P-016

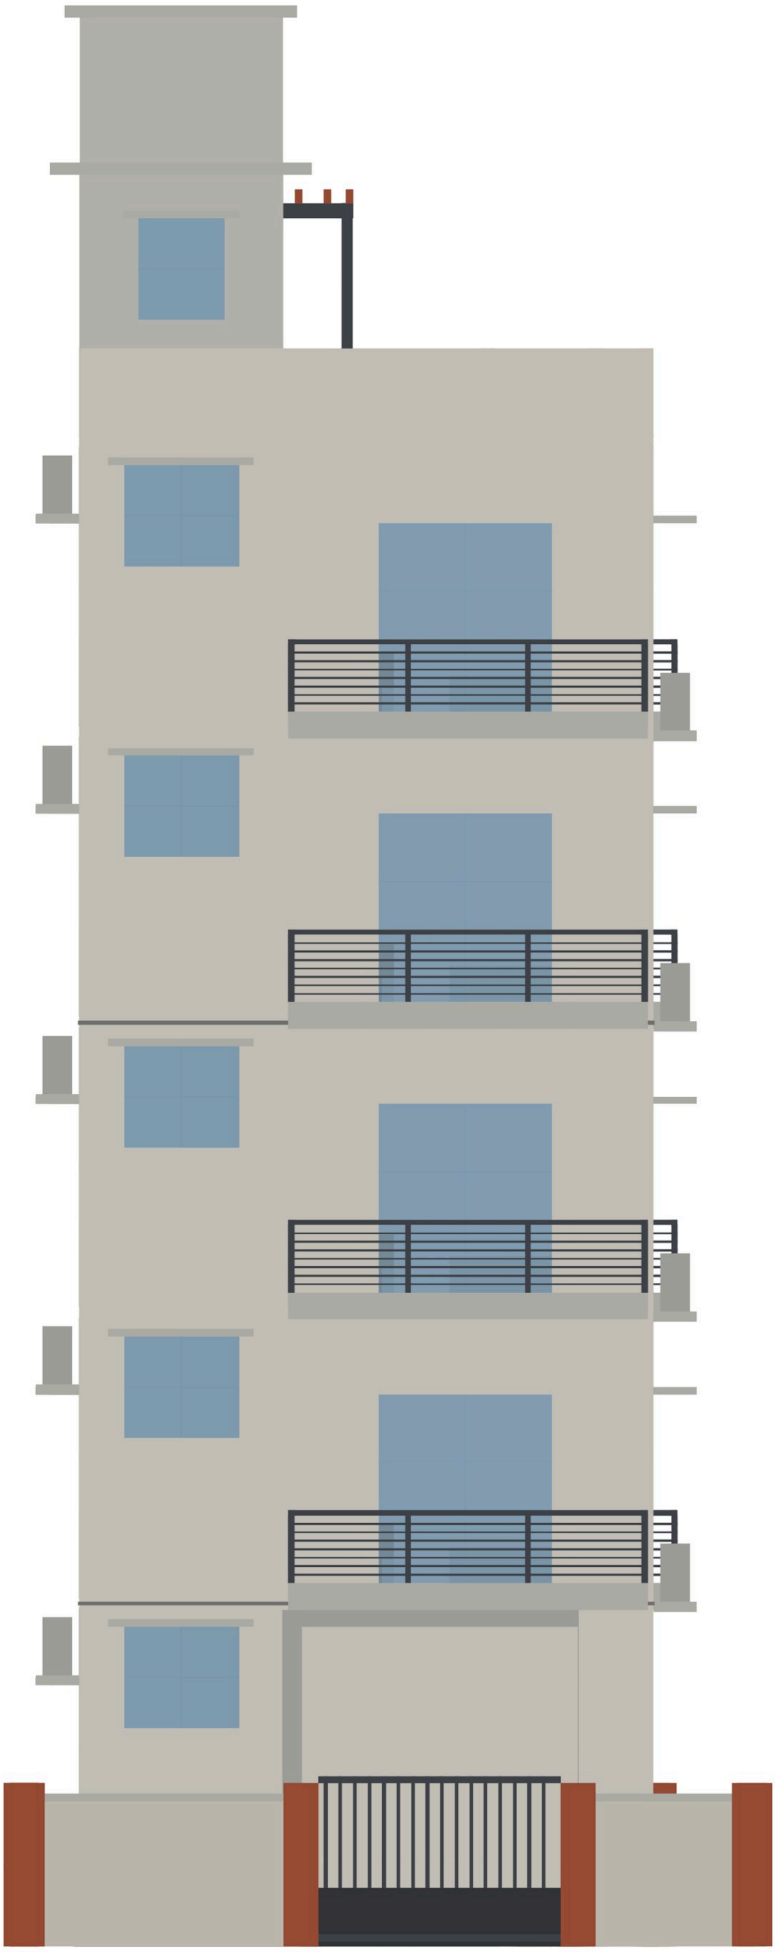

# PHASE 3 · LEFT SIDE ELEVATION · P-016

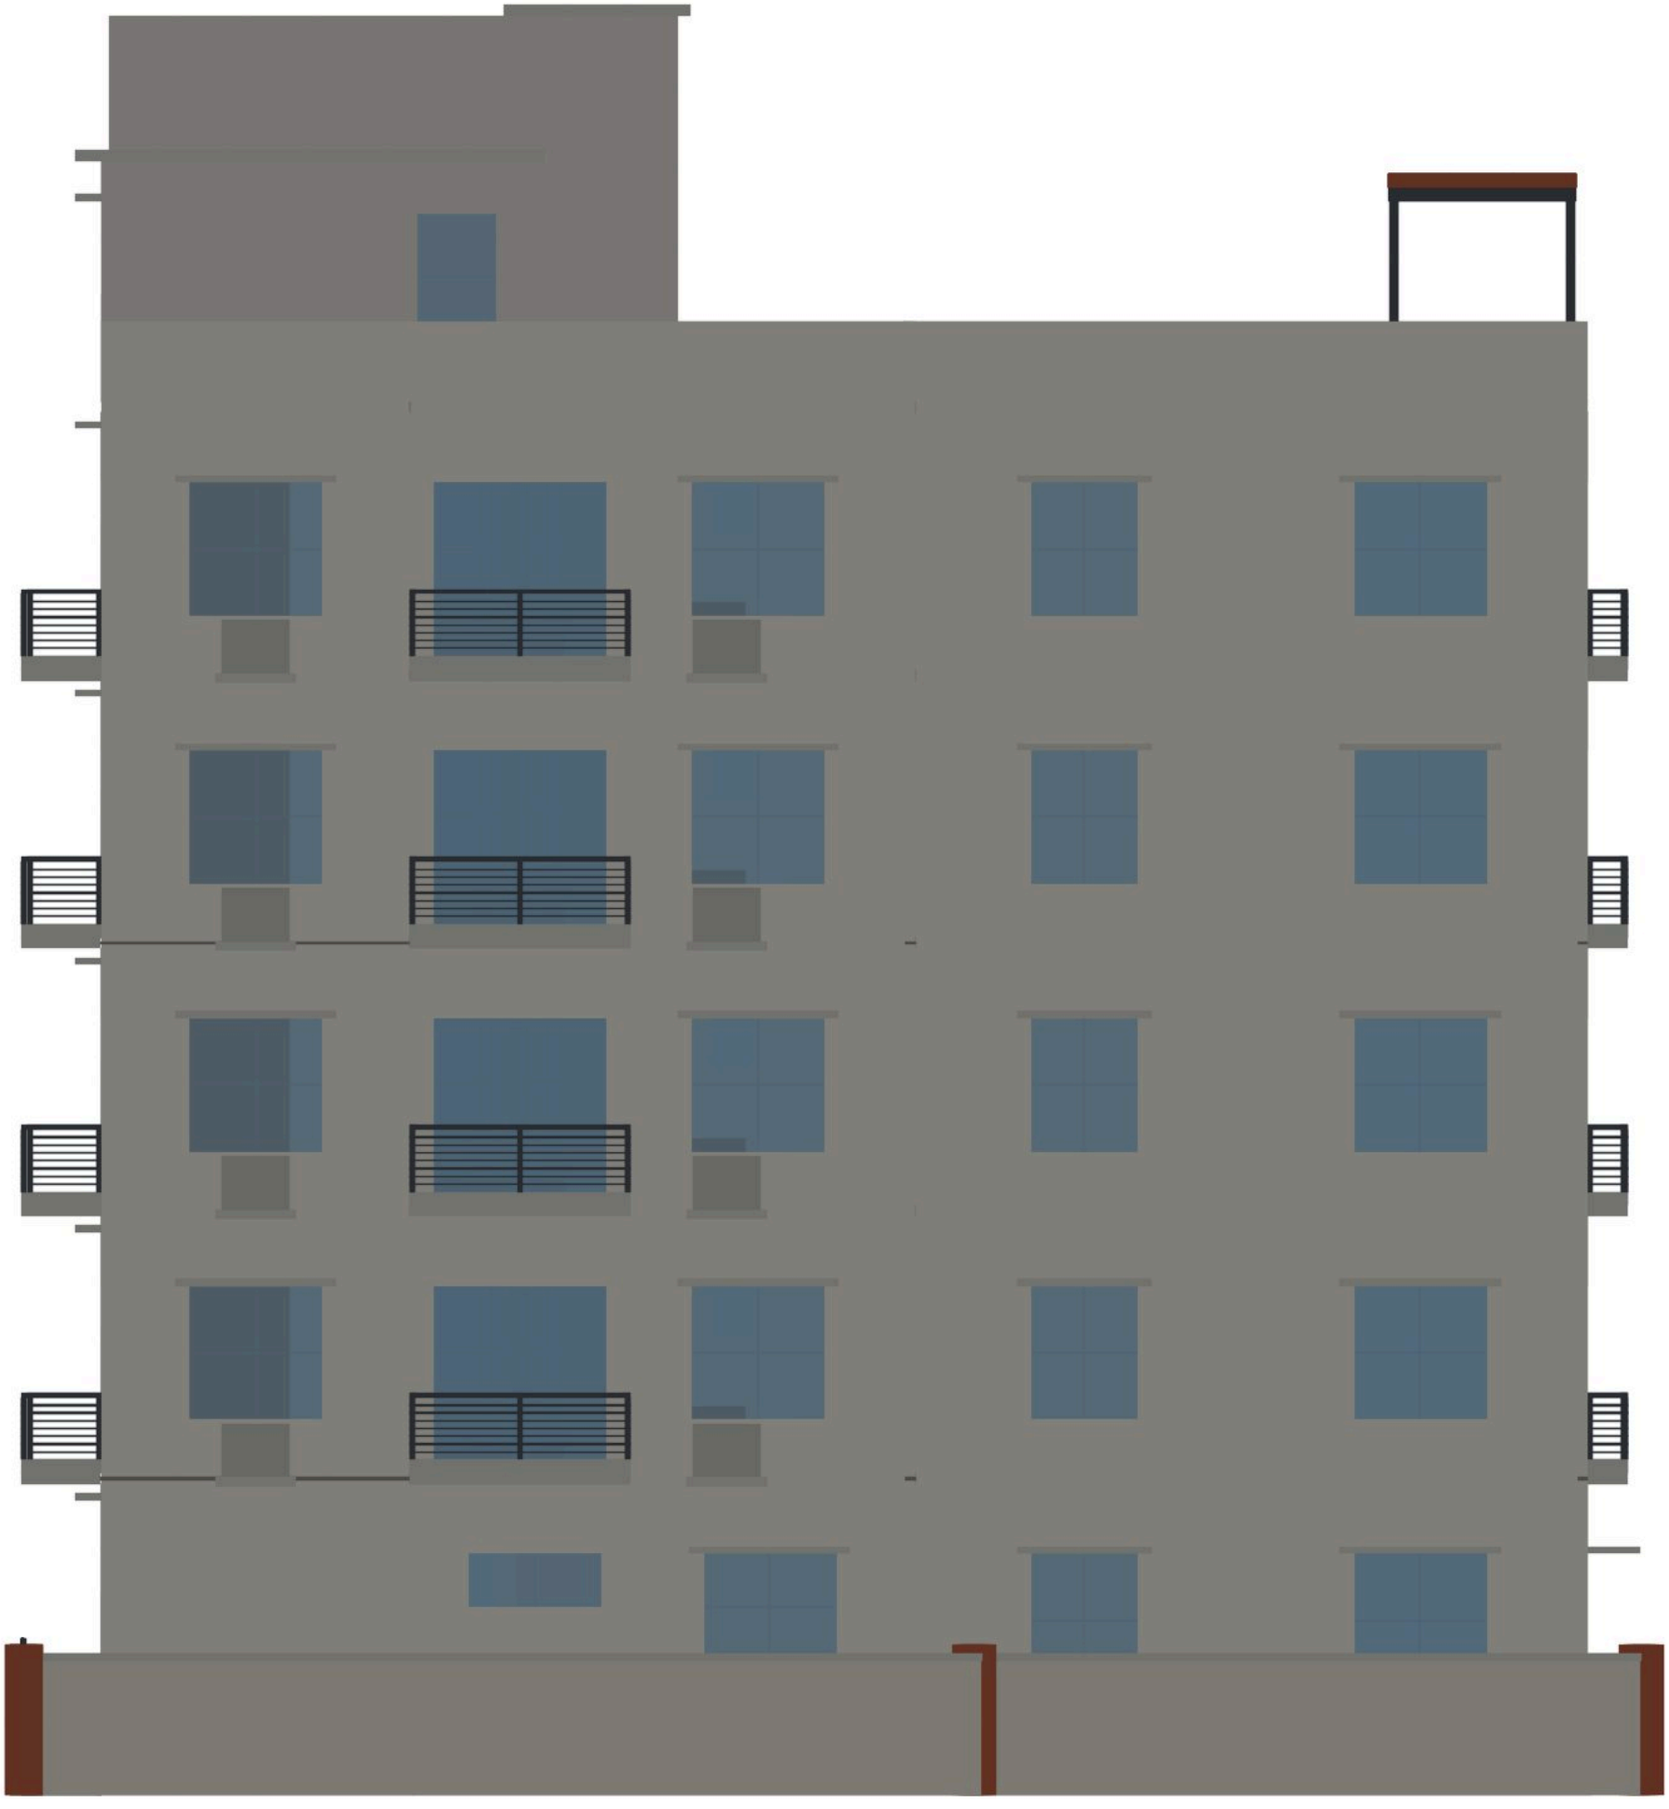

Phase 3 · views · render cutaway 1st floor






Phase 3 · views · render road right



Phase 4 · look B (TH-H01 Brick Pylon with White Shelves) · option B aerial



Phase 4 · look B (TH-H01 Brick Pylon with White Shelves) · option B back

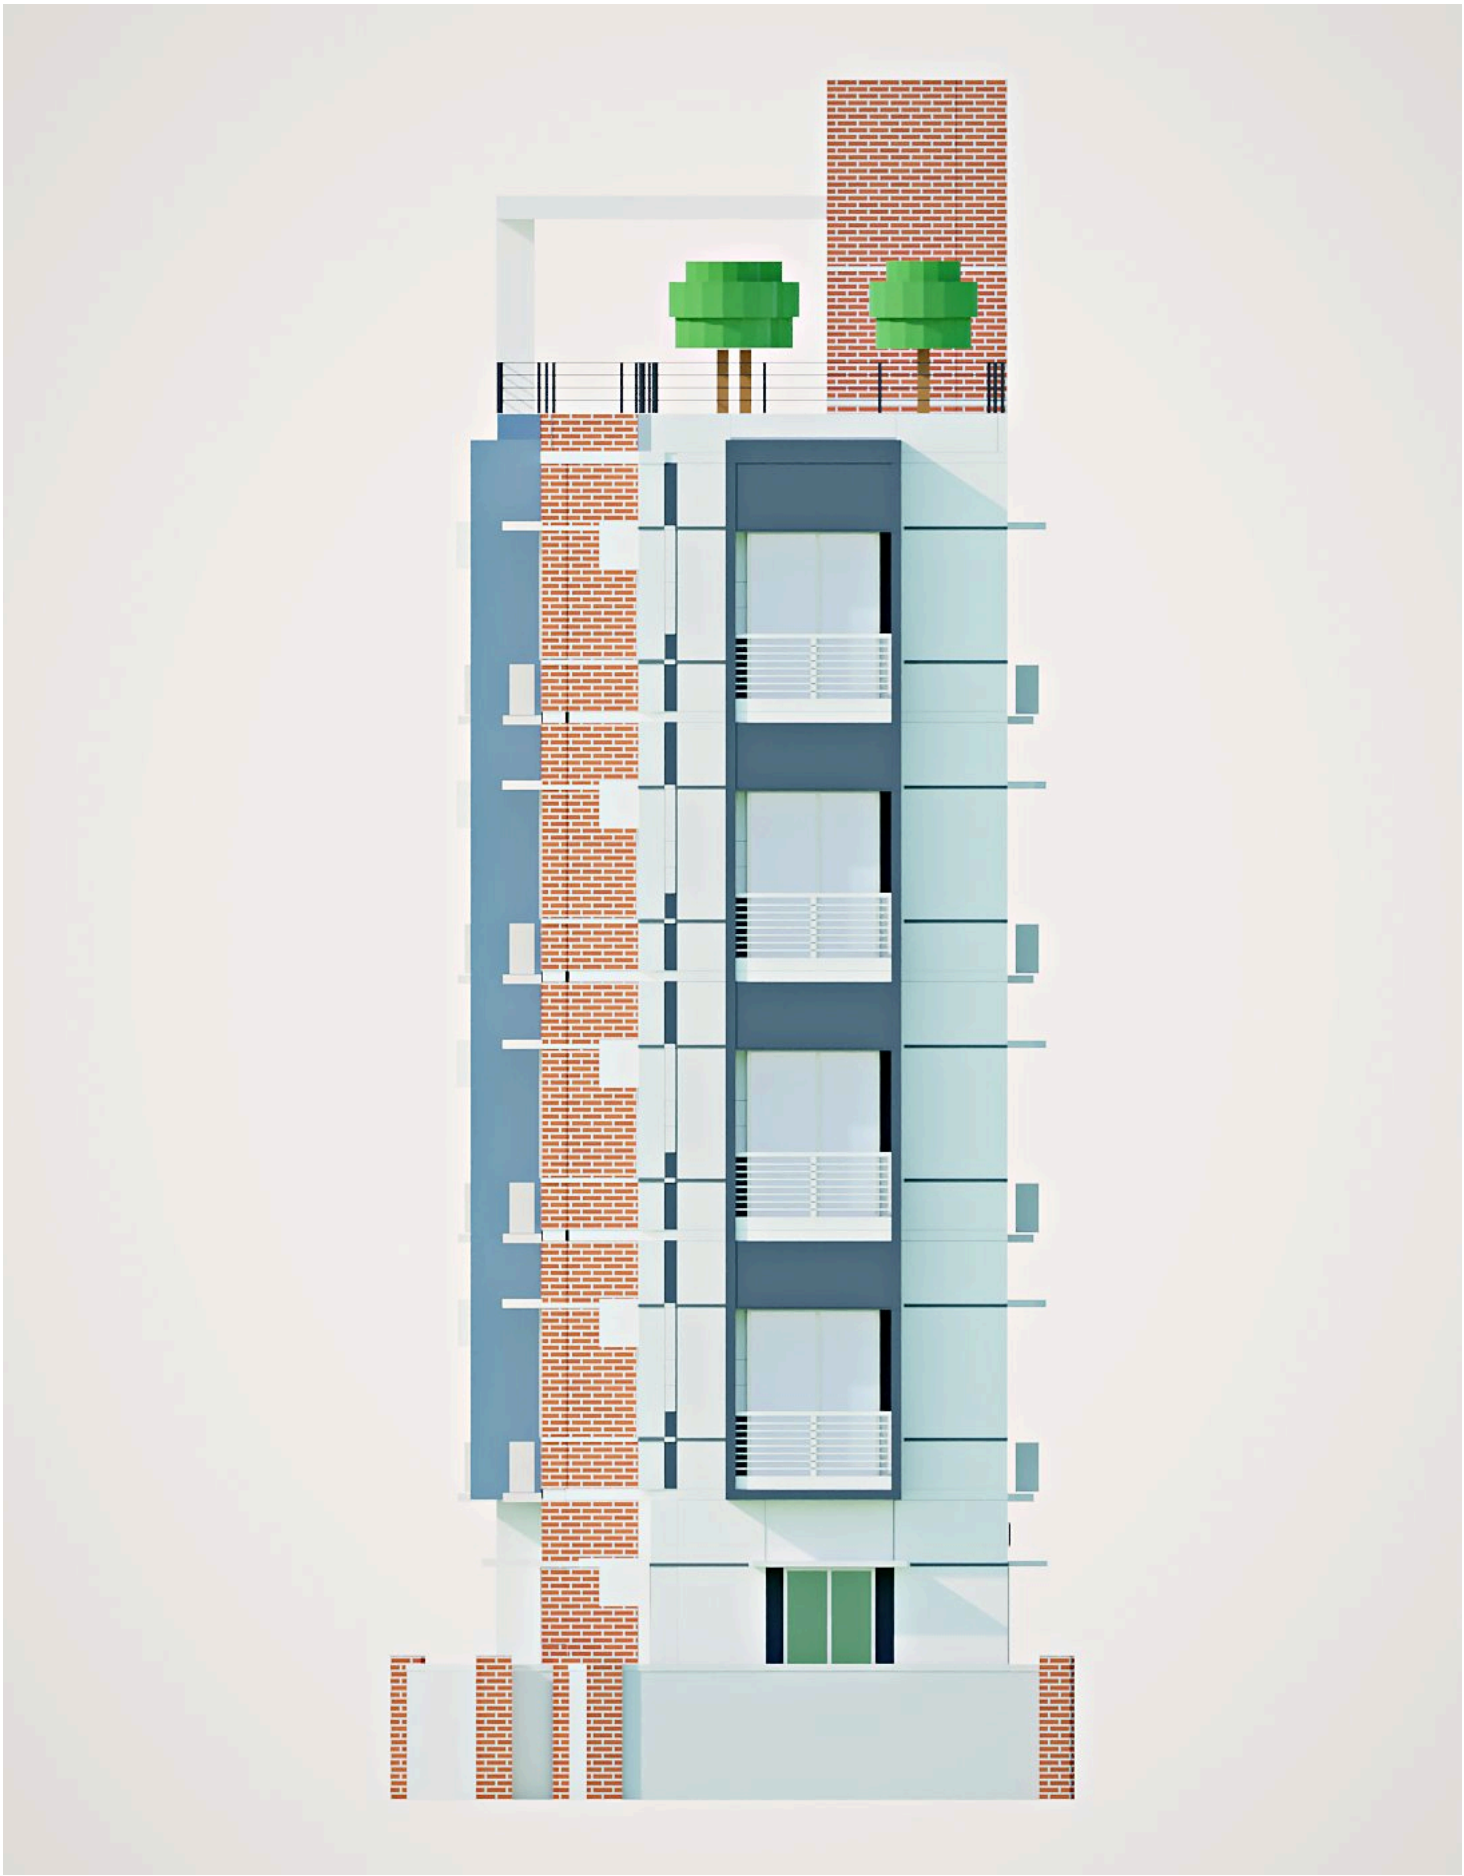


Phase 4 · look B (TH-H01 Brick Pylon with White Shelves) · option B back left



Phase 4 · look B (TH-H01 Brick Pylon with White Shelves) · option B back right



Phase 4 · look B (TH-H01 Brick Pylon with White Shelves) · option B front

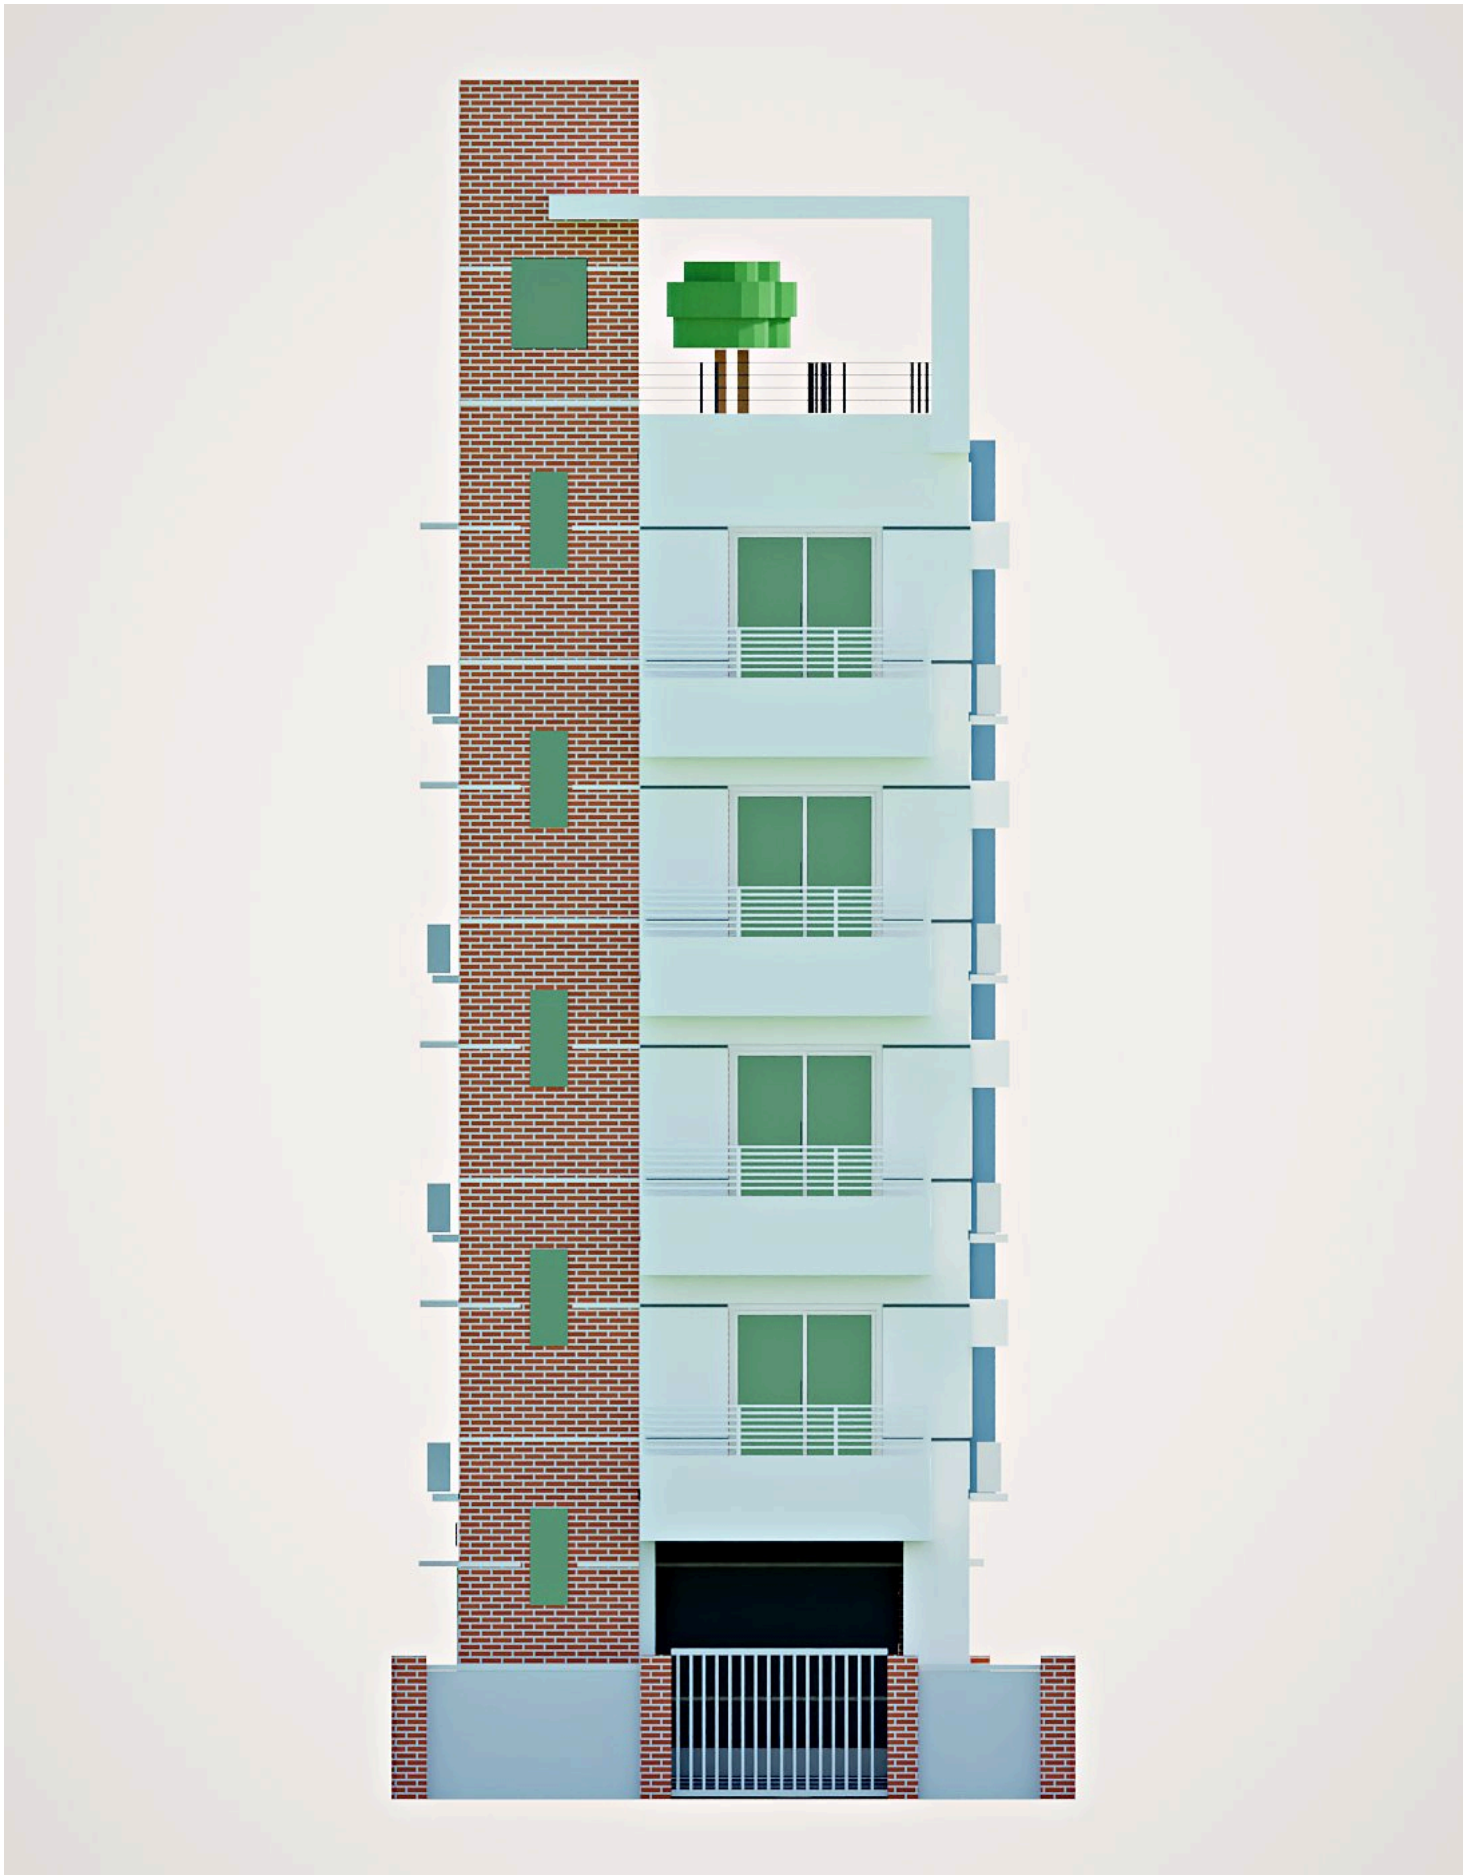

Phase 4 · look B (TH-H01 Brick Pylon with White Shelves) · option B hero left



Phase 4 · look B (TH-H01 Brick Pylon with White Shelves) · option B hero right



Phase 4 · look B (TH-H01 Brick Pylon with White Shelves) · option B road left




Phase 4 · look B (TH-H01 Brick Pylon with White Shelves) · option B road right



Phase 4 · look B (TH-H01 Brick Pylon with White Shelves) · option B side E




Phase 4 · look B (TH-H01 Brick Pylon with White Shelves) · option B side W

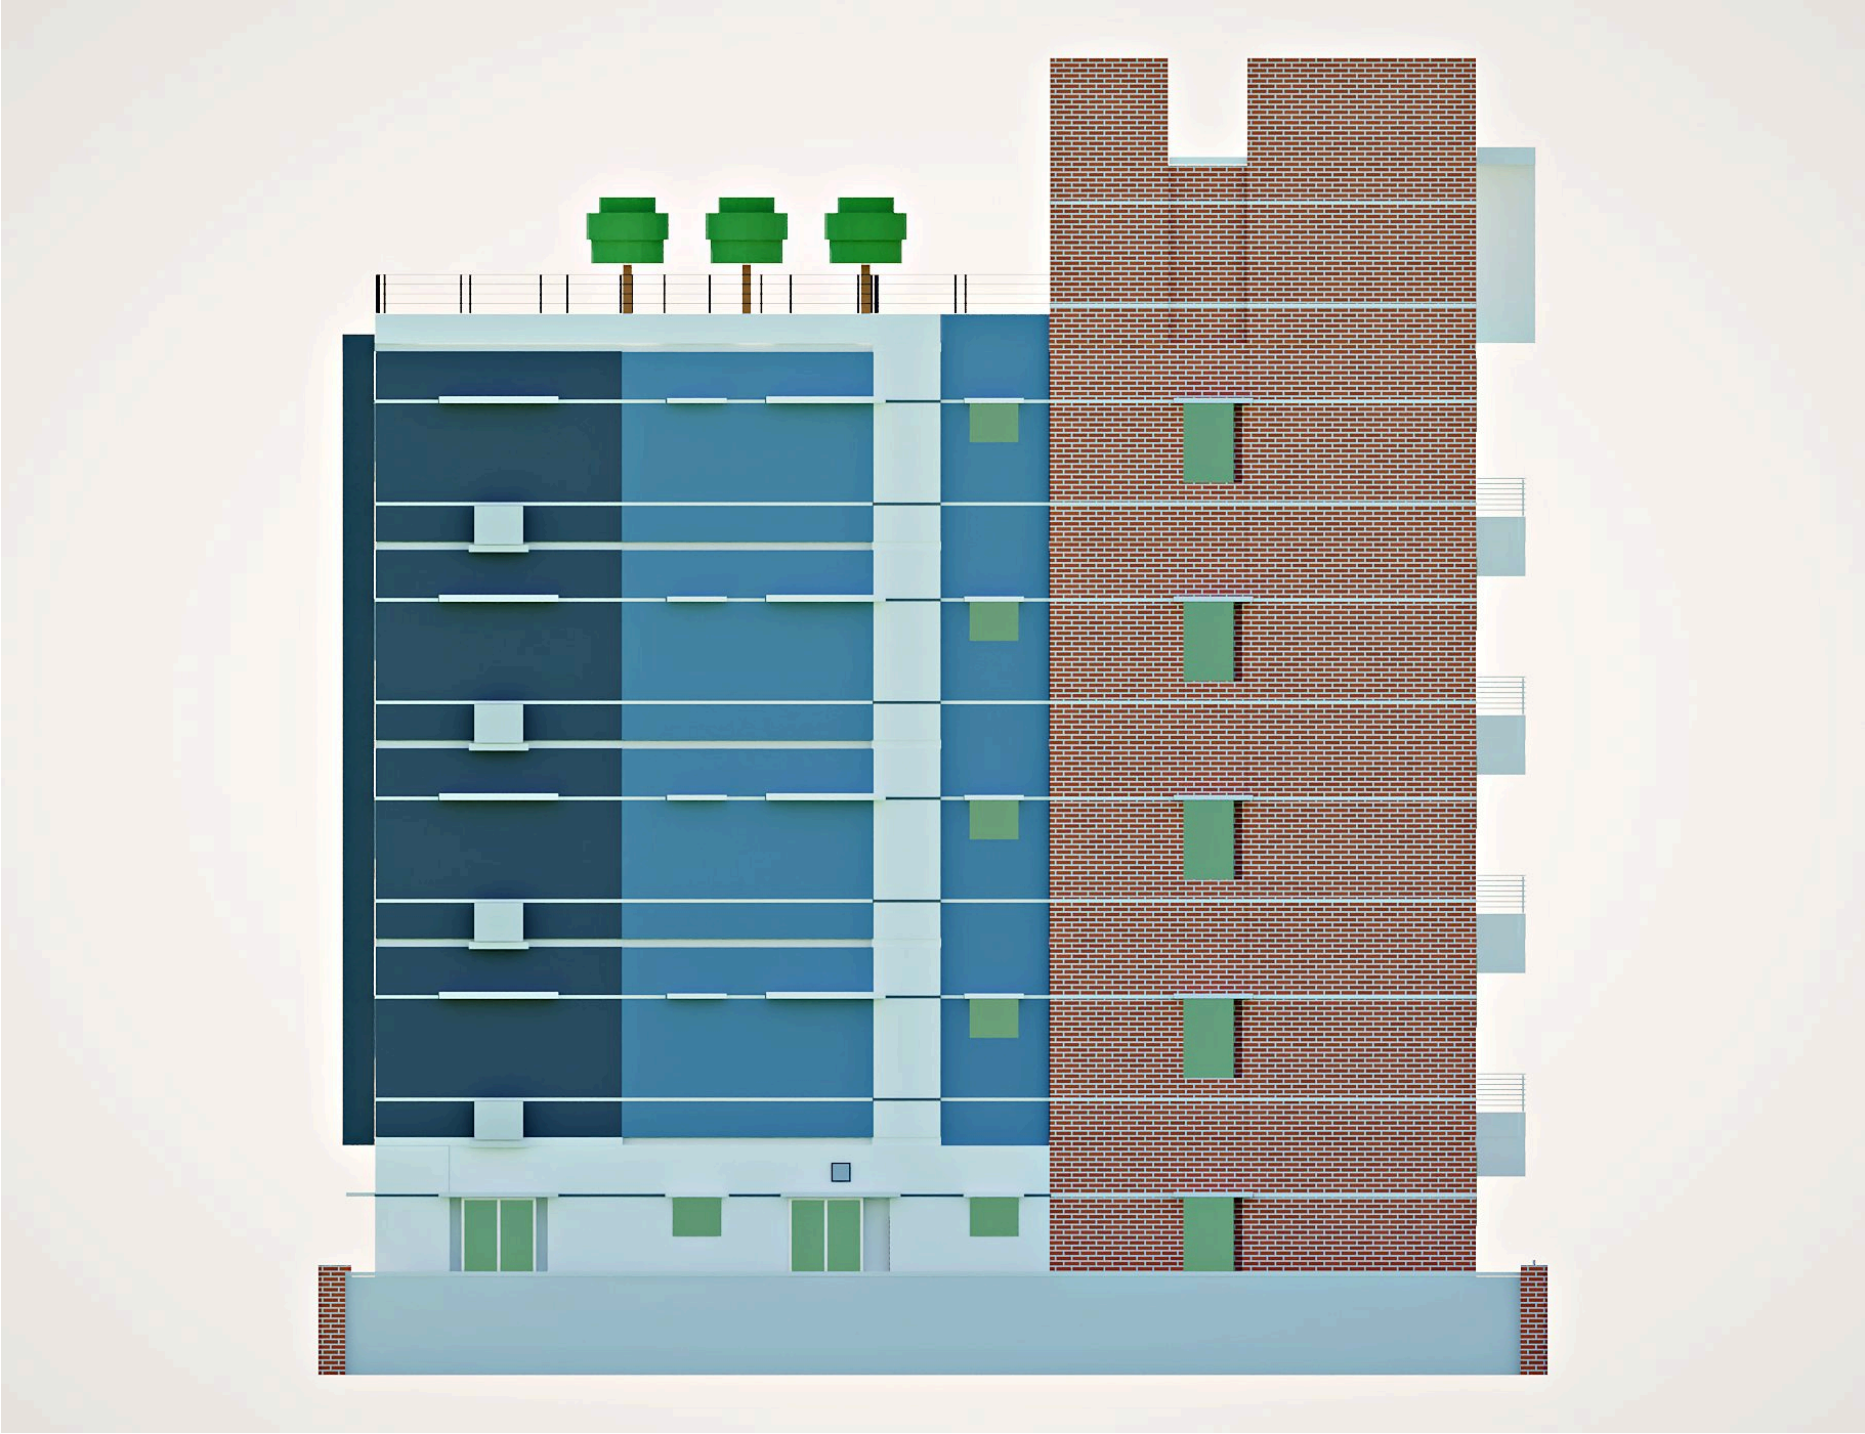

Phase 4 · look B (TH-H01 Brick Pylon with White Shelves) · option B street



Phase 5A · look B · P-016 5A 1st to 4th Floor 12Nov

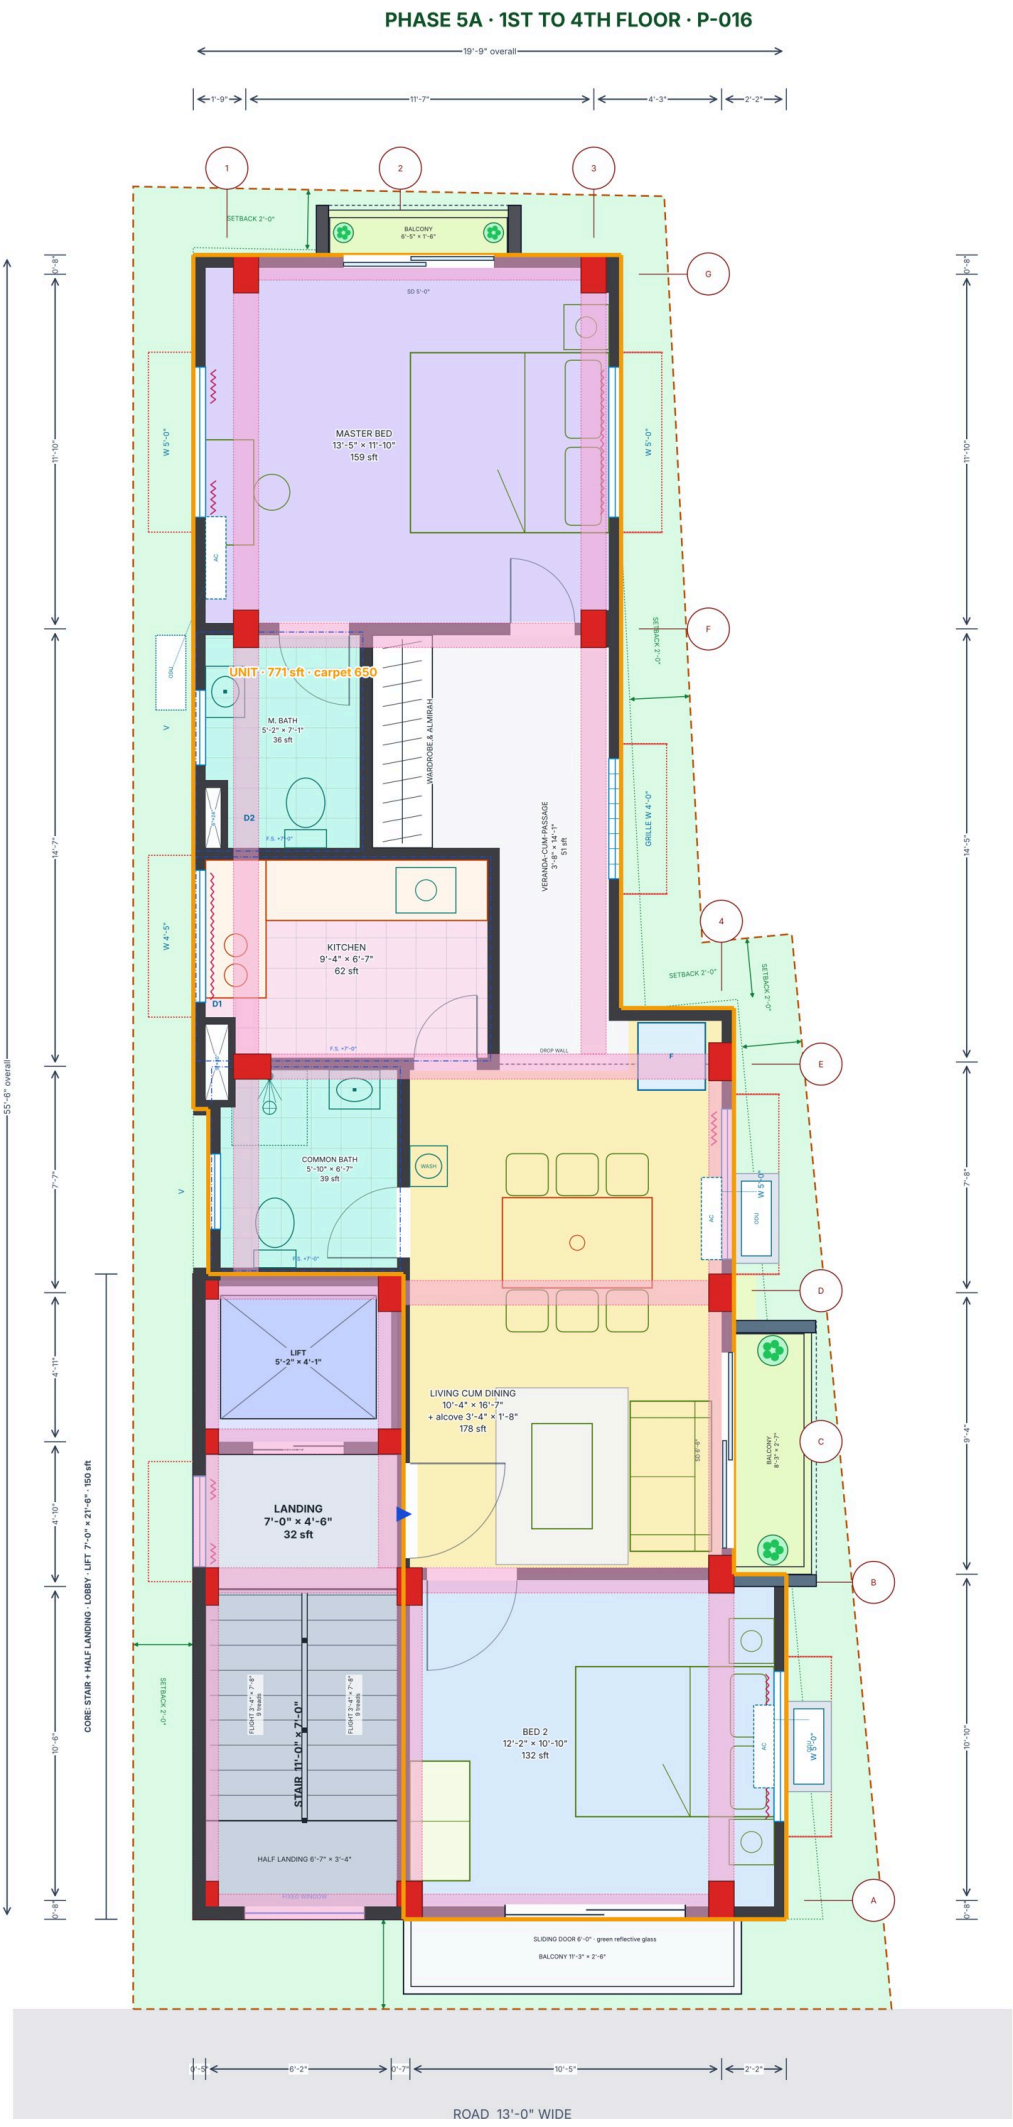


## ROOMS · Typical floor

inside sizes, face to face

**Bed 2**
10'-10" × 12'-2" · 132 sft

**Living cum Dining**
10'-4" × 16'-7" · 172 sft

**Common Bath**
6'-4" × 6'-7" · 42 sft


**Kitchen**
6'-7" × 9'-4" · 62 sft

**Veranda-cum-passage**
3'-8" × 14'-1" · 51 sft

**Master Bed Bath**
5'-2" × 7'-1" · 36 sft

**Master Bed**
11'-10" × 13'-5" · 159 sft

Phase 5A · look B · P-016 5A Ground Floor 12Nov

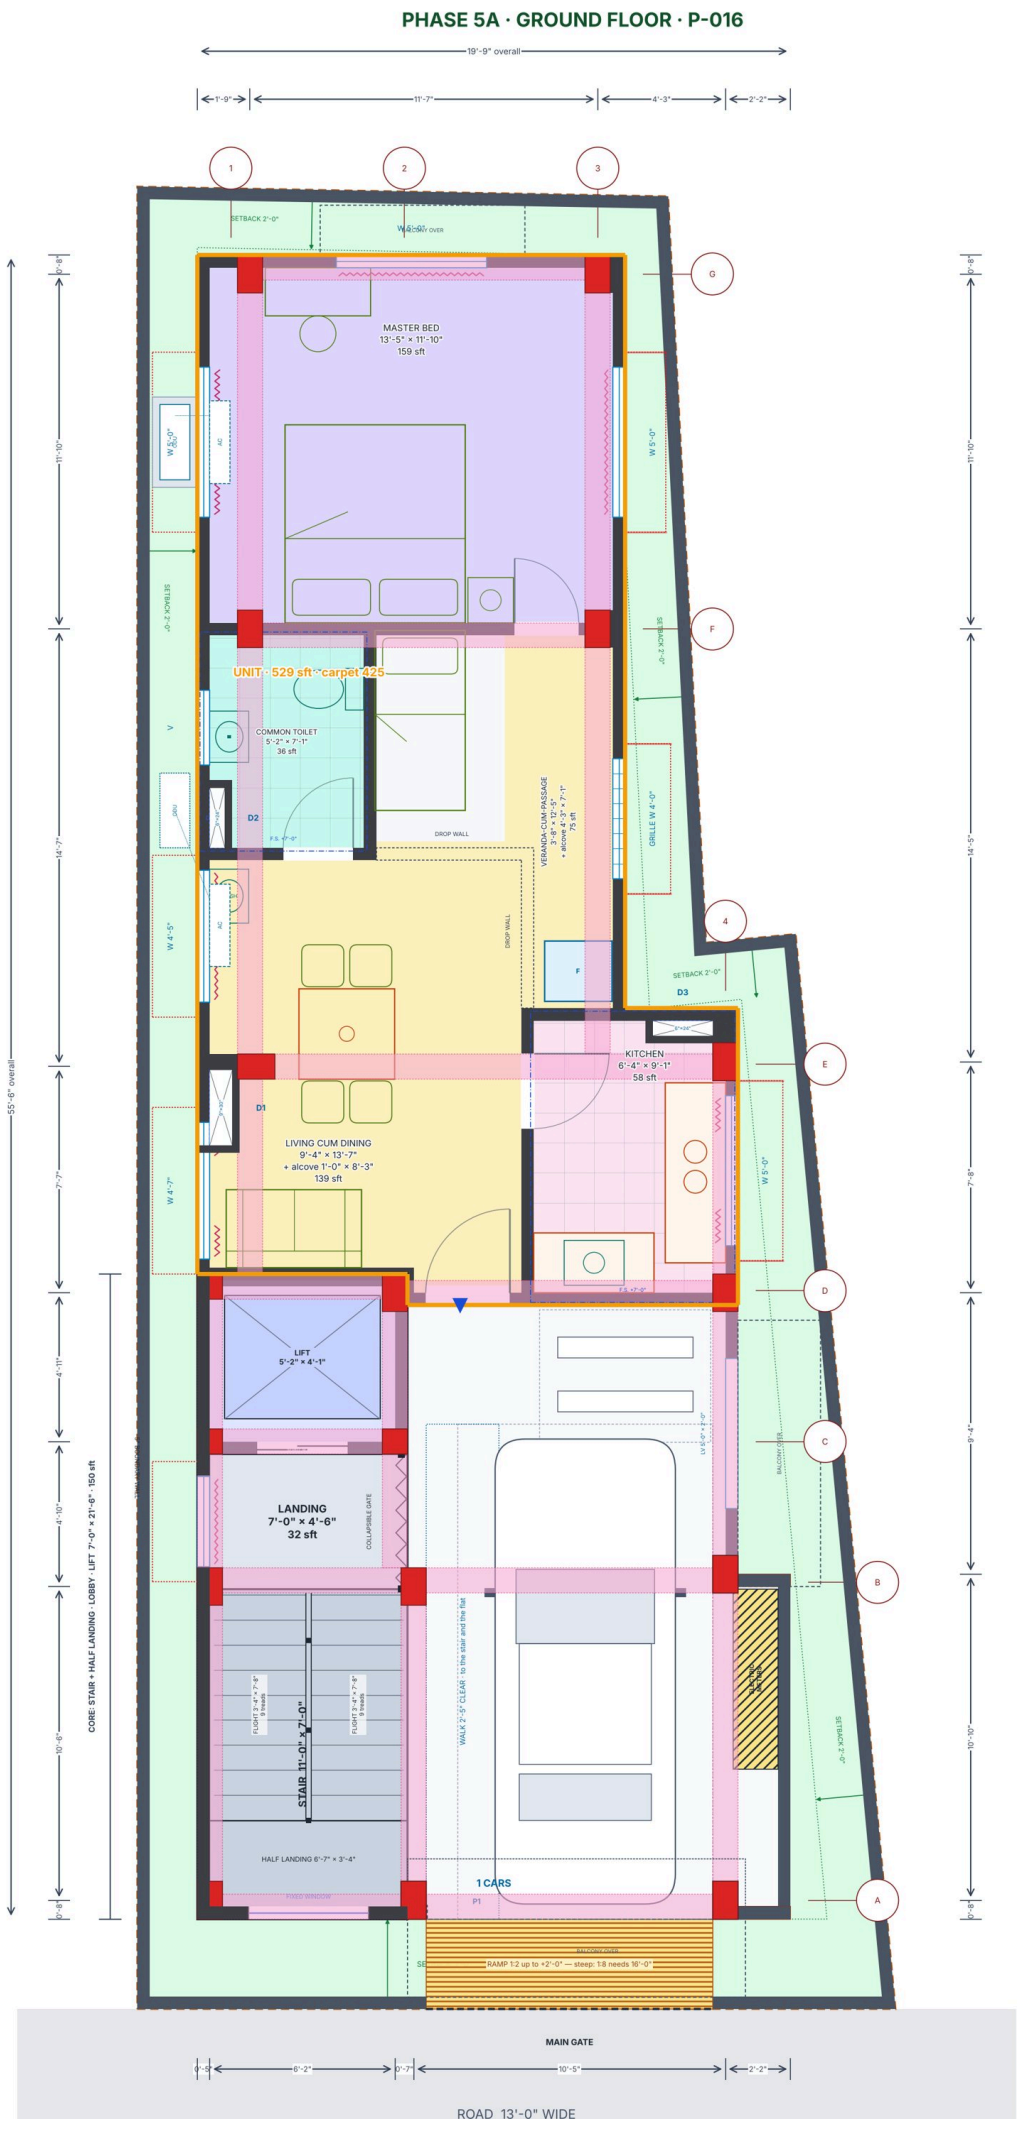


## ROOMS · Ground floor

inside sizes, face to face

**Living cum Dining**
9'-4" × 13'-7" · 127 sft


**Veranda-cum-passage**
3'-8" × 12'-5" · 45 sft

**Common Toilet**
5'-2" × 7'-1" · 36 sft

**Master Bed**
11'-10" × 13'-5" · 159 sft

**Kitchen**
6'-4" × 9'-1" · 58 sft

Phase 5A · look B · P-016 5A Roof 12Nov

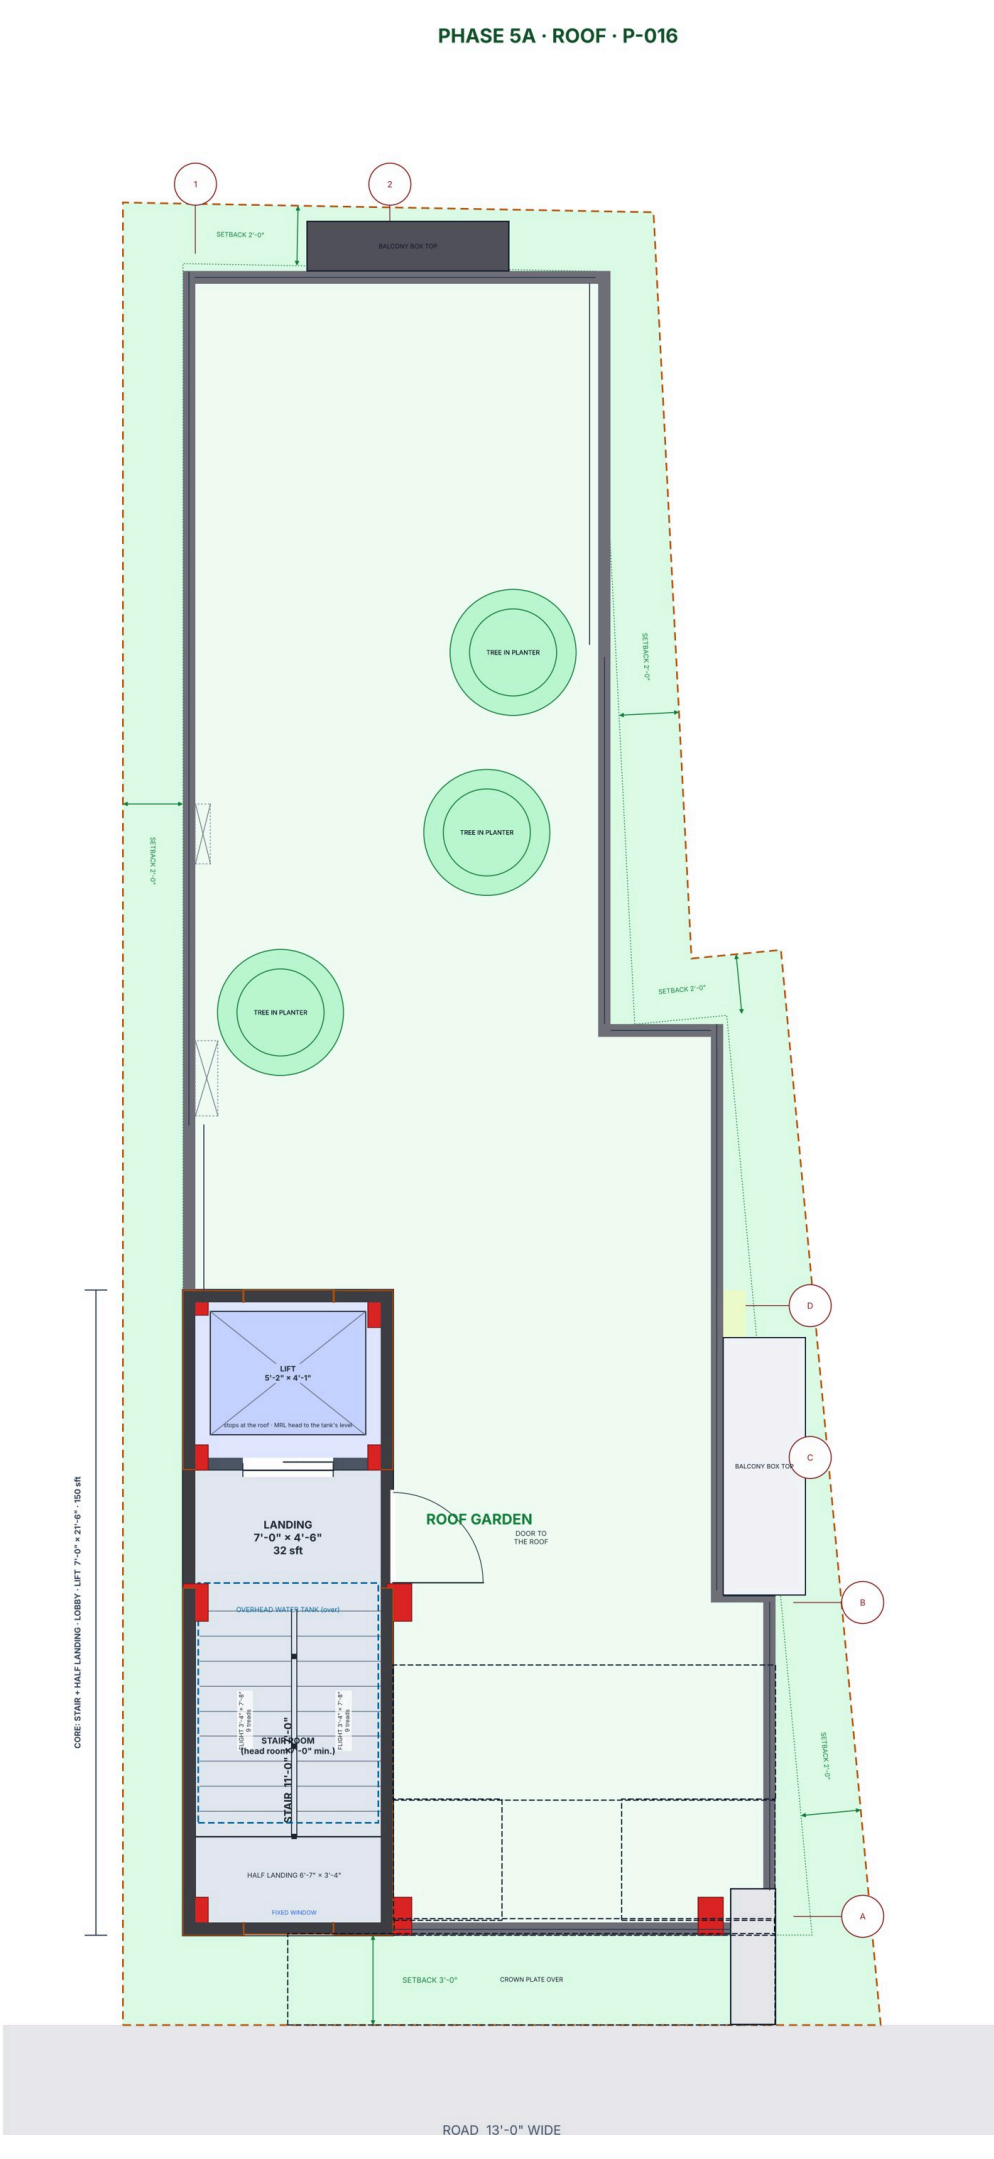


## ROOMS · Typical floor

inside sizes, face to face

**Bed 2**
10'-10" × 12'-2" · 132 sft

**Living cum Dining**
10'-4" × 16'-7" · 172 sft

**Common Bath**
6'-4" × 6'-7" · 42 sft

**Kitchen**
6'-7" × 9'-4" · 62 sft


**Veranda-cum-passage**
3'-8" × 14'-1" · 51 sft

**Master Bed Bath**
5'-2" × 7'-1" · 36 sft

**Master Bed**
11'-10" × 13'-5" · 159 sft

Phase 5A · look B · P-016 5A Top View 12Nov

# PHASE 5A · TOP VIEW · P-016

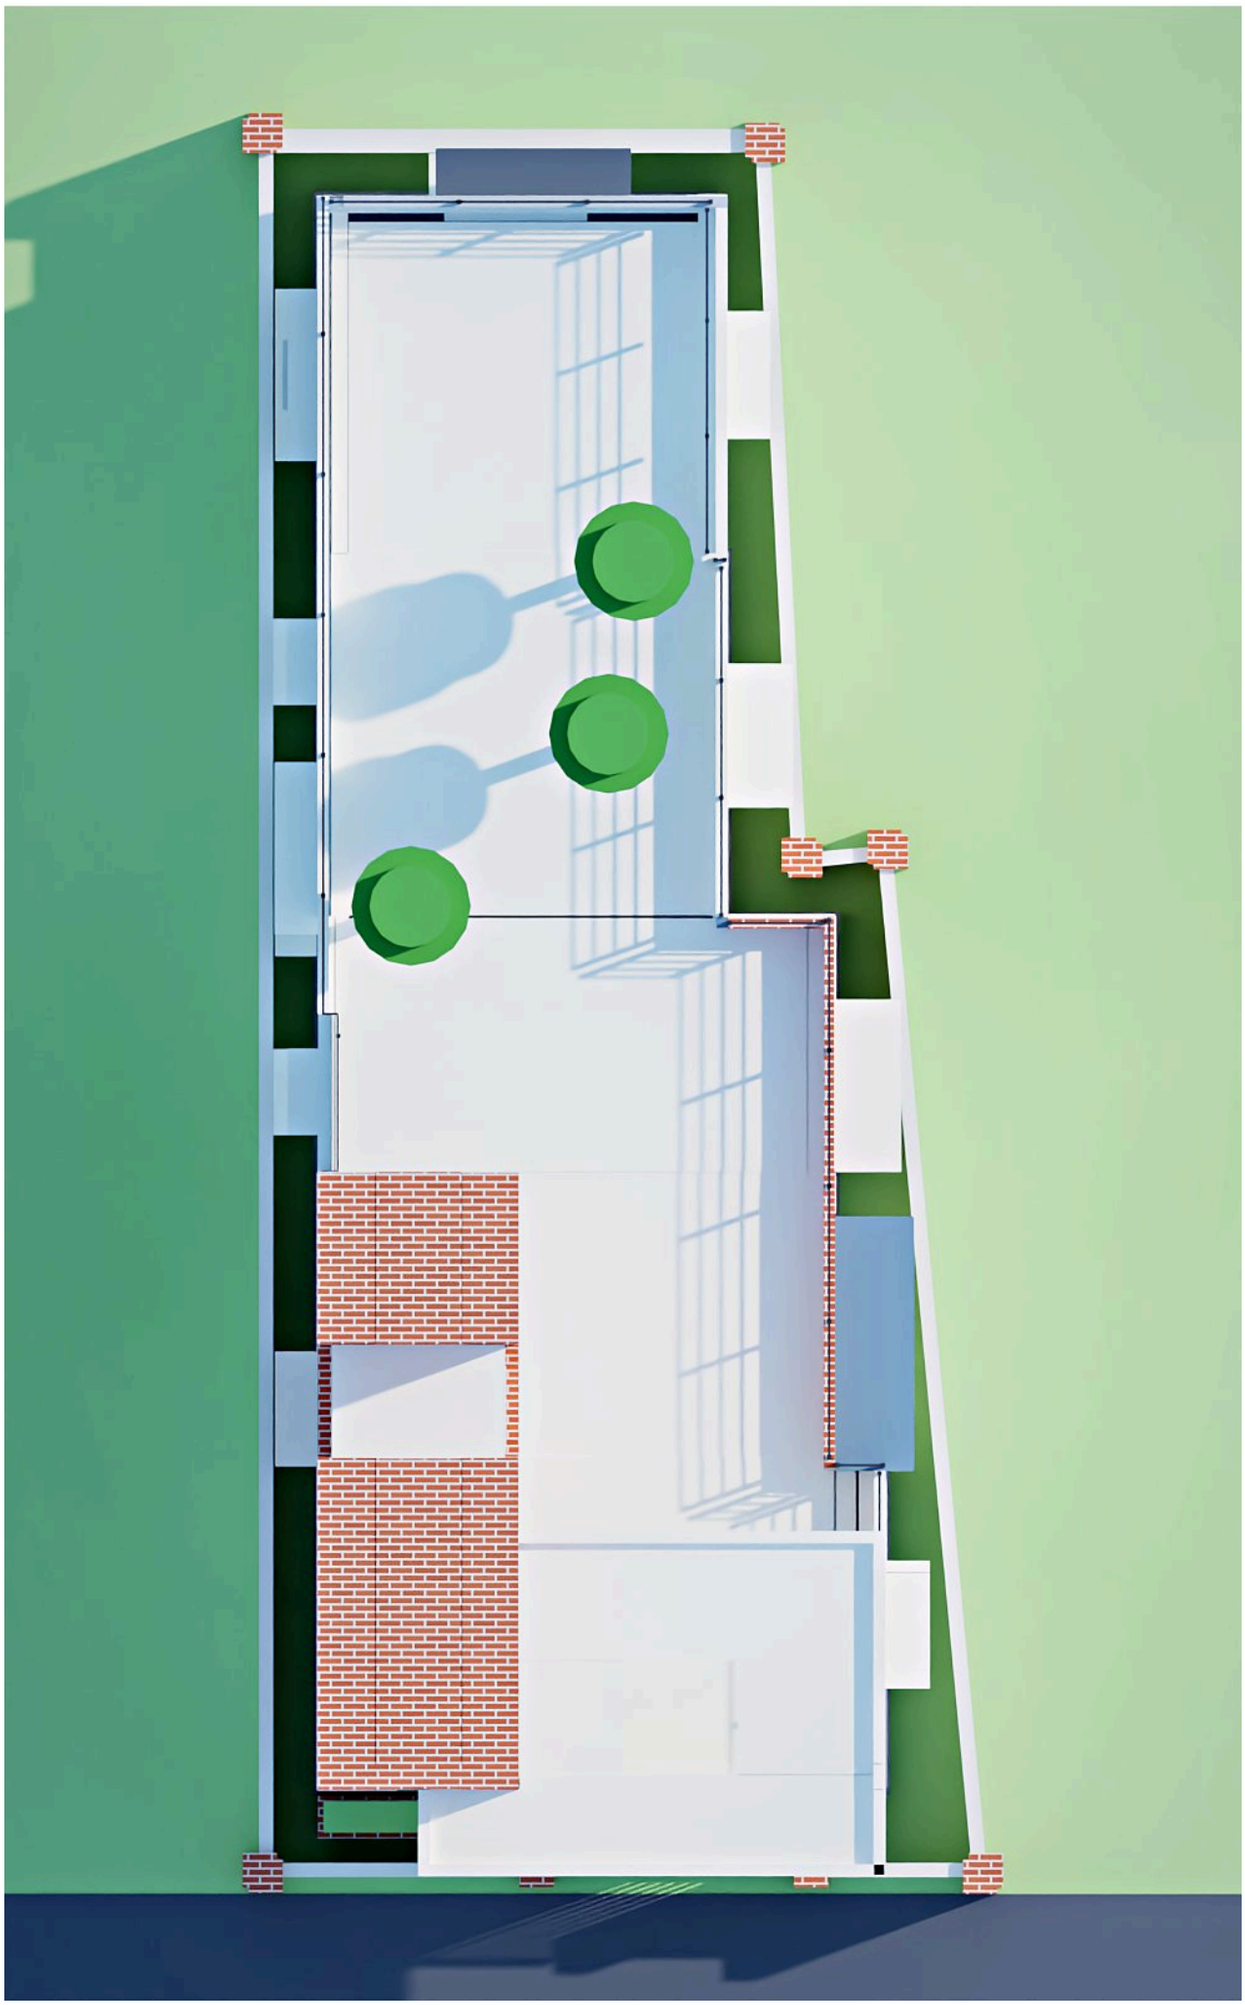

## ROOMS · Typical floor

inside sizes, face to face

**Bed 2**
10'-10" × 12'-2" · 132 sft

**Living cum Dining**
10'-4" × 16'-7" · 172 sft

**Common Bath**
6'-4" × 6'-7" · 42 sft

**Kitchen**
6'-7" × 9'-4" · 62 sft

**Veranda-cum-passage**
3'-8" × 14'-1" · 51 sft

**Master Bed Bath**
5'-2" × 7'-1" · 36 sft

**Master Bed**
11'-10" × 13'-5" · 159 sft